
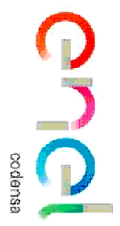
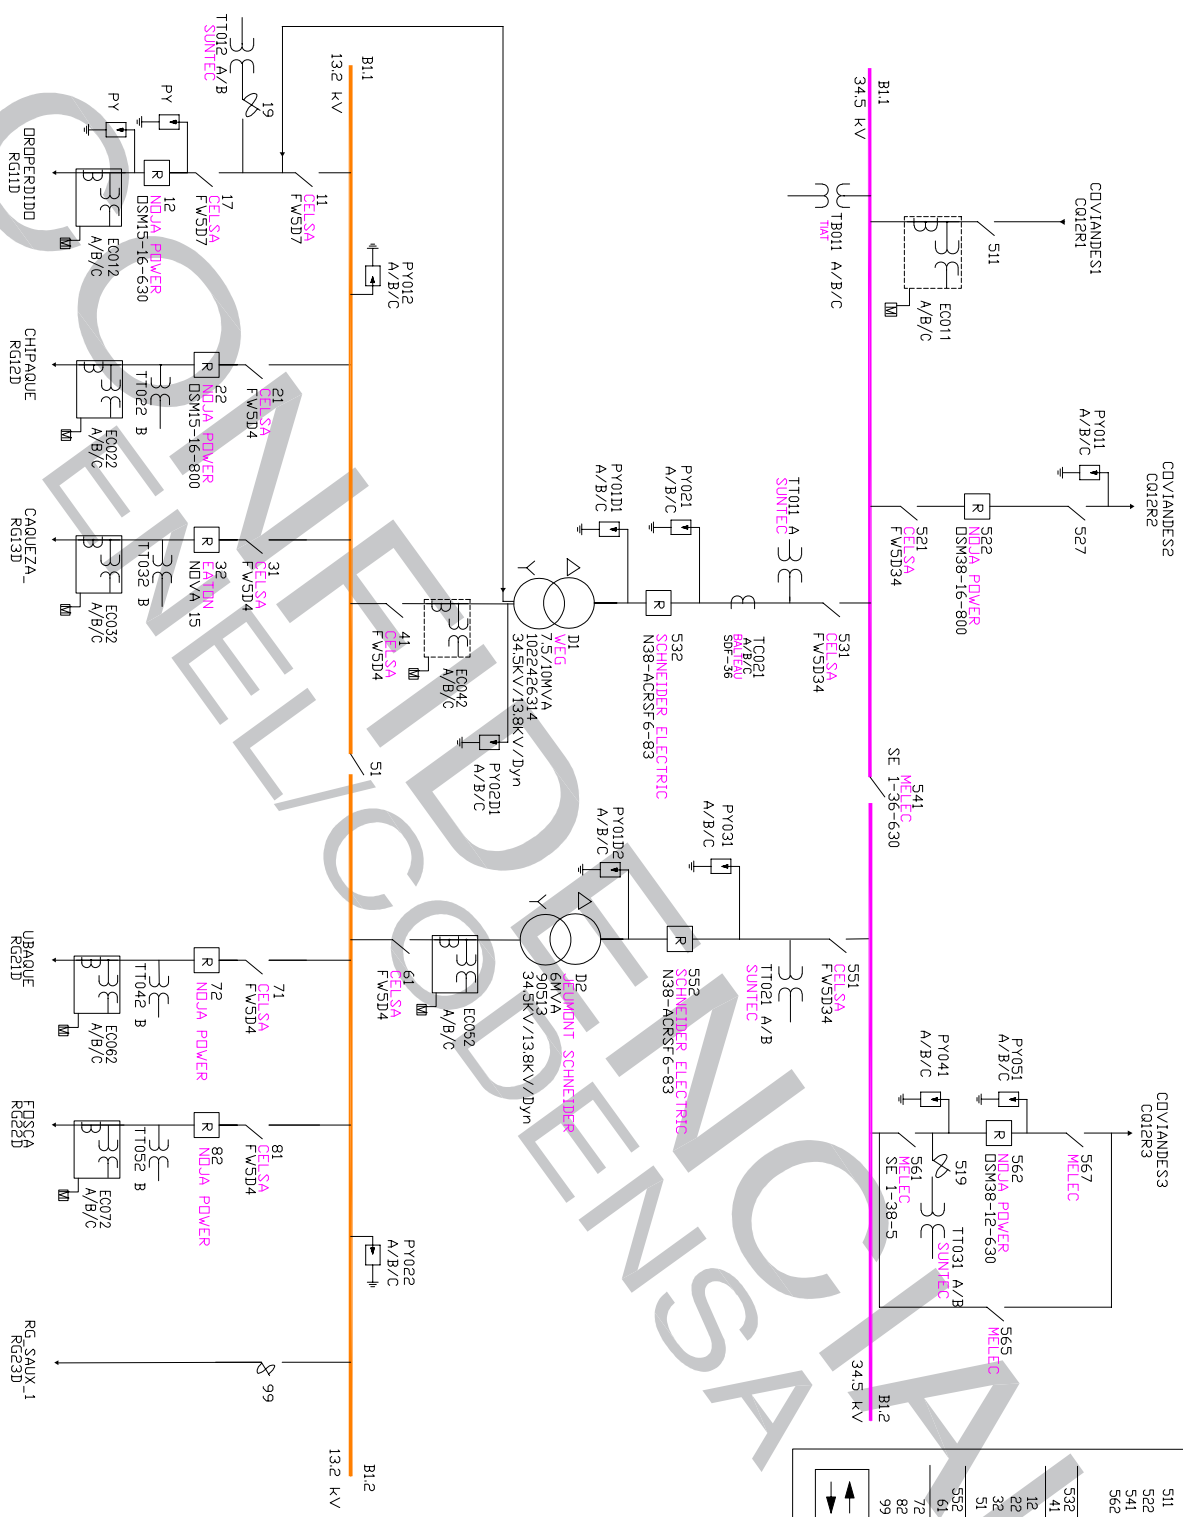


511	CO1R1	COVIANDES1	→
522	CO1R2	COVIANDES2	→
541	UB B11, B12	COVIANDES3	→
562	CO1R3	MEDIDA B11	→
532	D1	WEG 7.5/10 MVA	
41	D2	WEG 7.5/10 MVA	
12	RG1D	OROPERDIDO	
22	RG1D	CHIPPAQUE	
32	RG1D	CAQUEZA	
51	UB B11, B12		
552	D2	JEUMONT SCHNEIDER 6/7.5MVA	
61	D2	JEUMONT SCHNEIDER 6/7.5MVA	
72	RG21D	UBAQUE	
82	RG22D	FUSCA	
99	RG23D	RG-SAUX_1	
→ POTENCIA DE ENTRADA			
→ POTENCIA DE SALIDA			

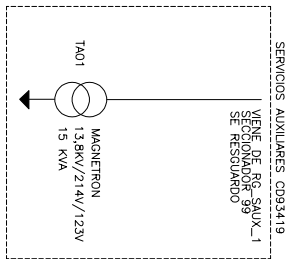

Unidad Organizativa
Administración Informática
Técnica Col

REVISION No.	11	DIAGRAMA UNIFILAR	125
FECHA:	SEPTIEMBRE/2022	SUBESTACION RESGUARDO	HOLIA: 1
ARCHIVO:	RESGUARDO.DWG	MUNICIPIO DE CAQUEZA	DE: 1
C:\ESQUEMAS SUBESTACIONES\CONTROL UNIFILARES		CODIGO: RG	