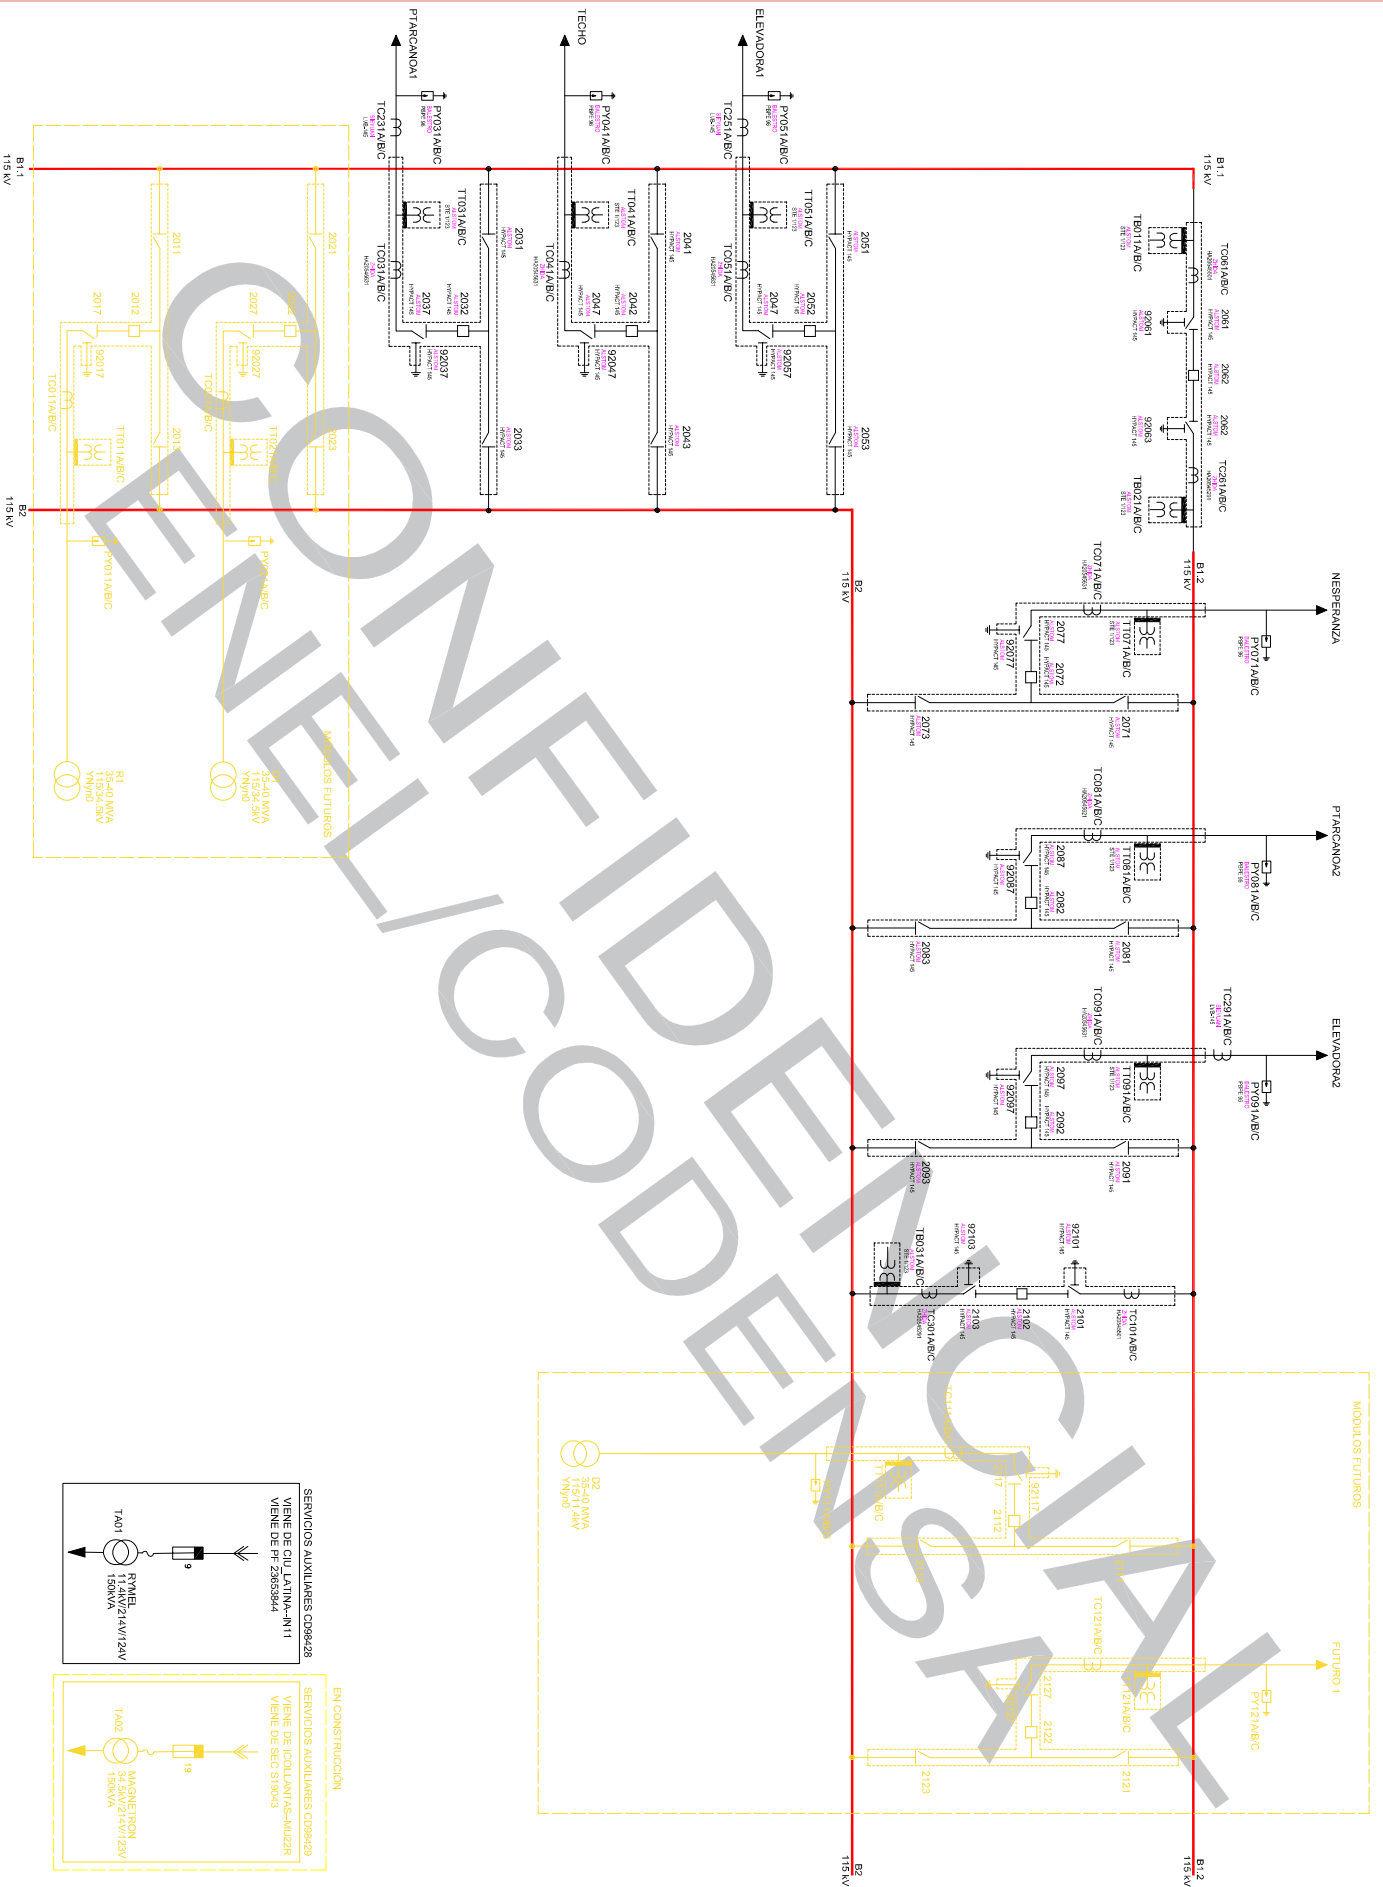


Unidad Organizativa
Administración Informática
Técnica Col.

REVISION No. 4
FECHA: NOVIEMBRE/2022
ARCHIVO: RIO.DWG
\\COLCDD09FS01\FilesServer\CONTROL UNIFILARES

DIAGRAMA UNIFILAR
SUBESTACION RIO
Variante Soacha-Mondoñedo al lado
de la PTAR Canoas, municipio de Soacha

143
HOU: 2
DE: 2