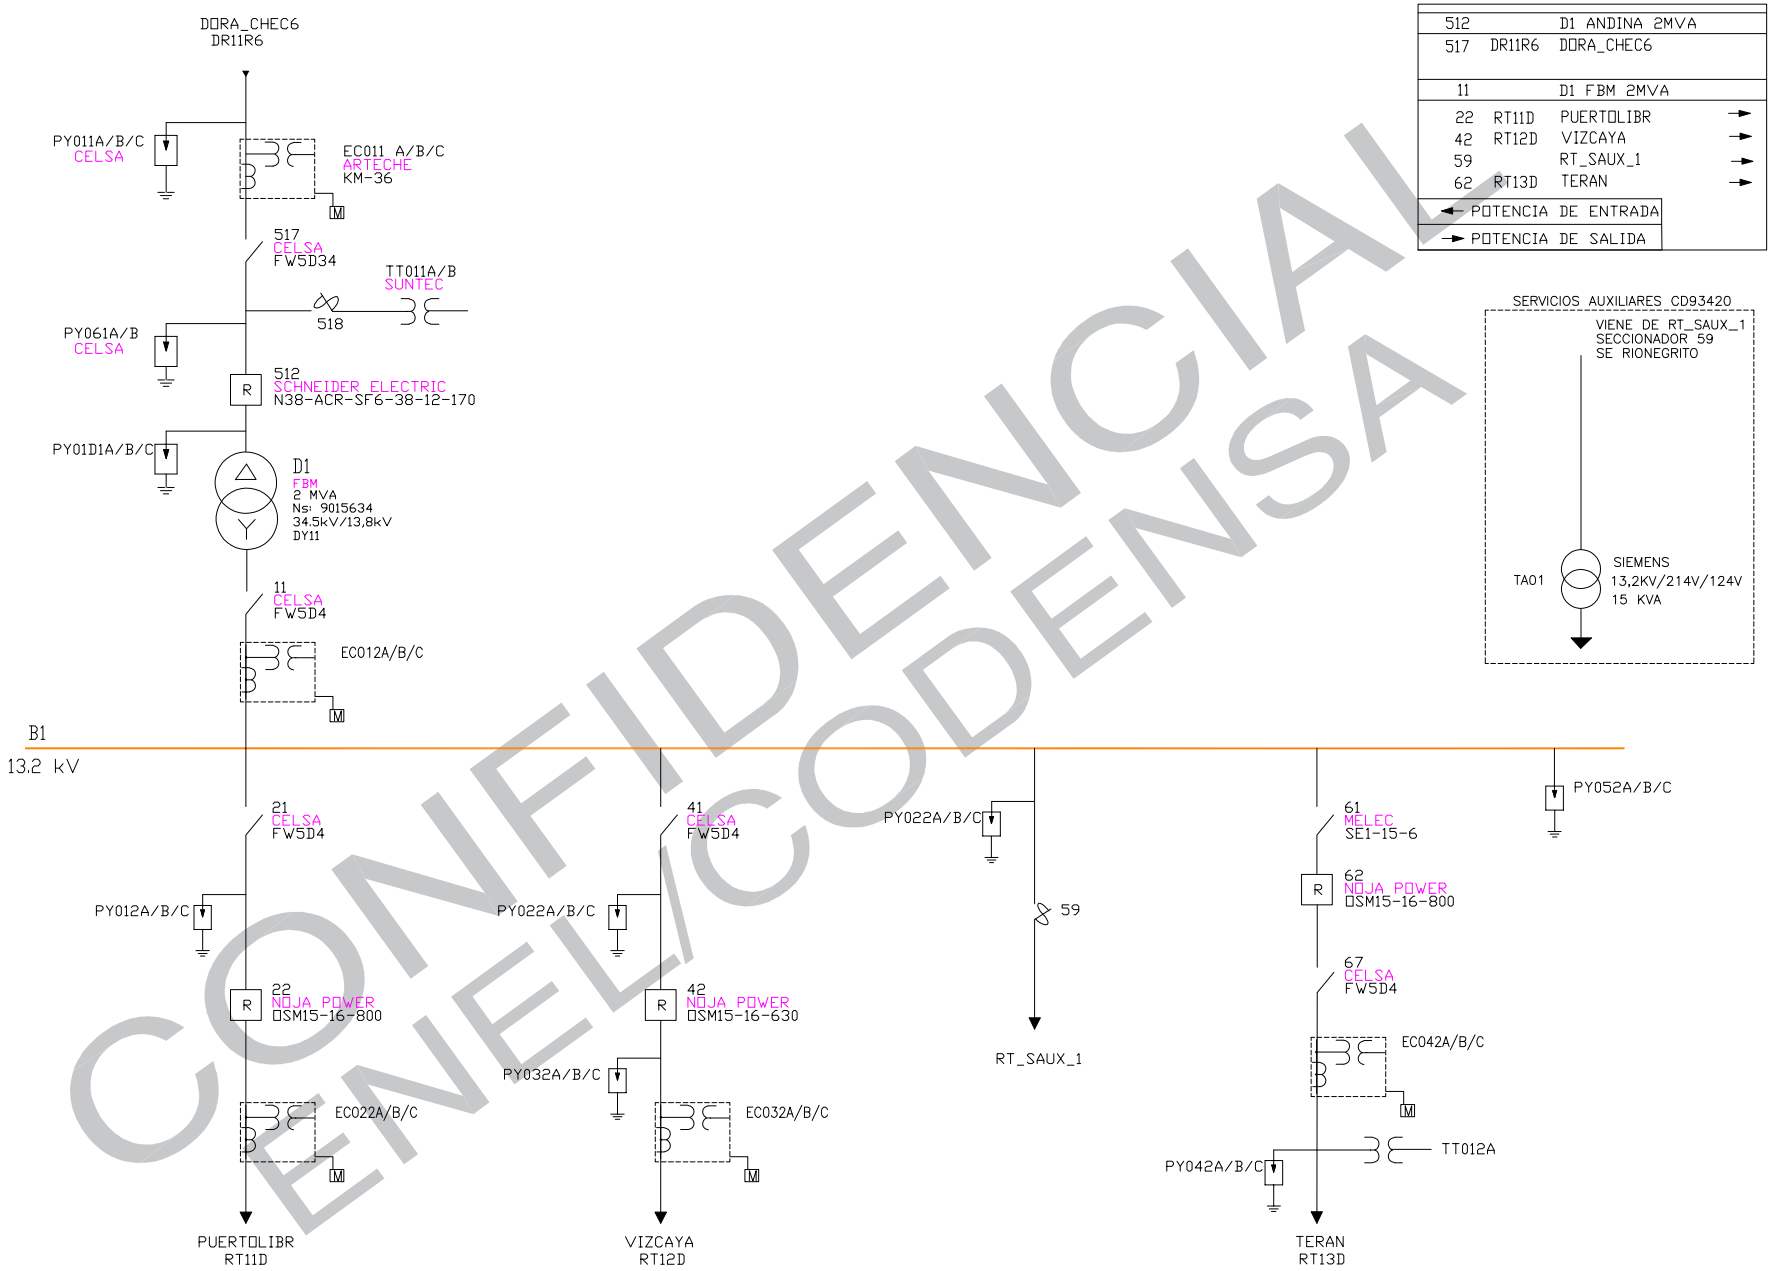

CONFIDENCIAL
ENEL/CODENSA

Unidad Organizativa Administraciòn Informaciòn Tècnica Col	REVISION No. 6	DIAGRAMA UNIFILAR SUBESTACION RIONEGRITO MUNICIPIO PUERTO SALGAR	622
	FECHA: FEBRERO/2022		HOJA: 1
	ARCHIVO: RIONEGRITO.DWG C:\ESQUEMAS SUBESTACIONES\ESQUEMAS DEFINITIVOS	CODIGO: RT	DE: 1