

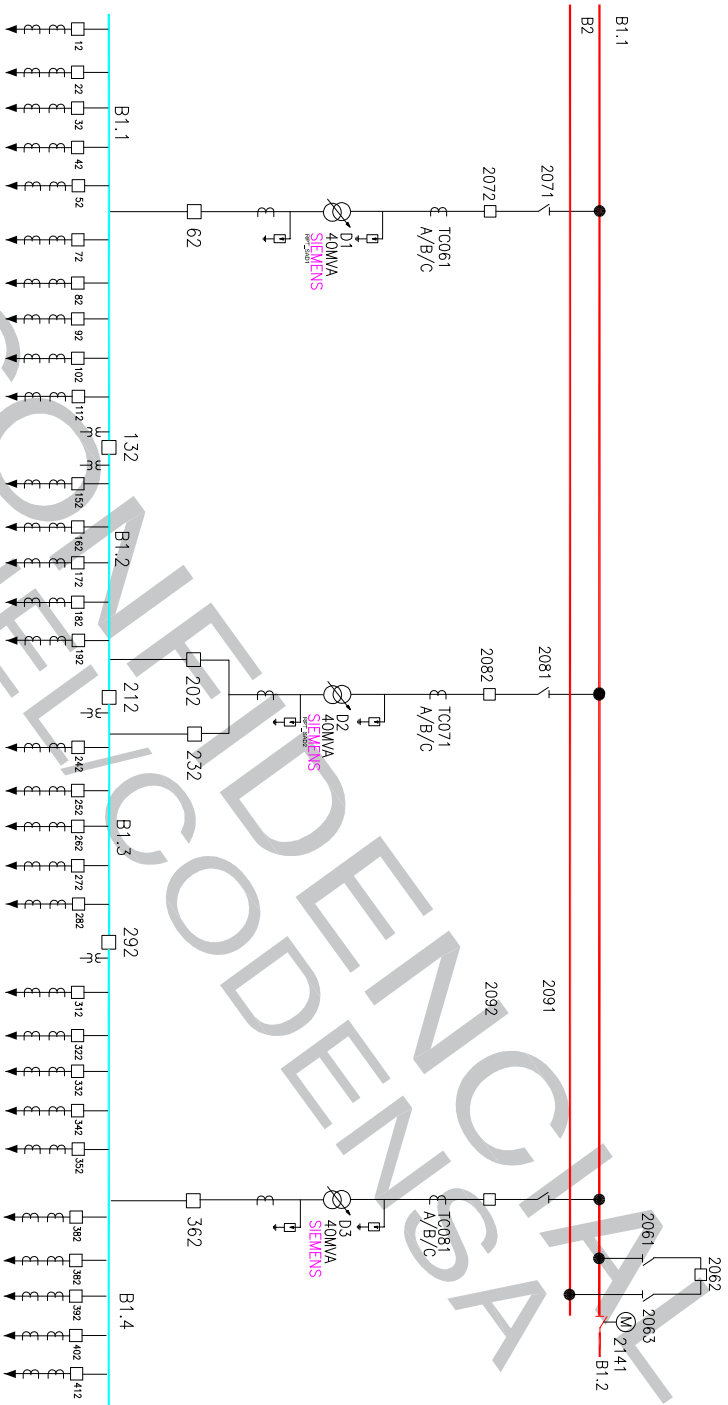
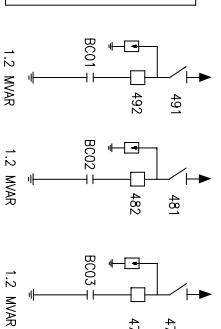
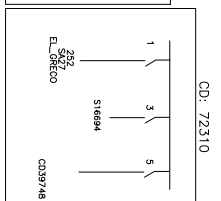
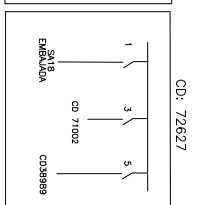
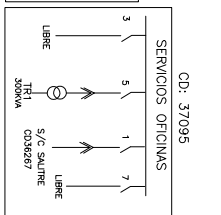
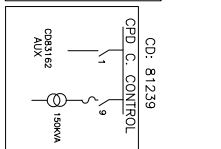
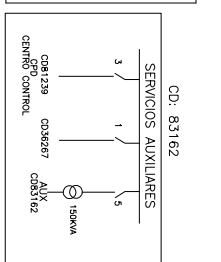
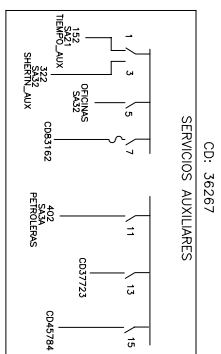


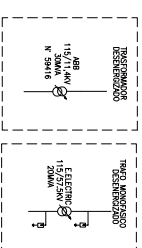

12	SA11 CAMBIEA	→	C01
12	SA12 DESARROLLO	→	C01
32	SA13 XEROX	→	C03
42	SA14 NORMANDIA	→	C04
52	SA15 ST. CECILIA	→	C05
62	D1 SIEMENS 40 MVA	→	C06
72	SA16 ALUMINOS	→	C07
82	SA17 EL GREGO	→	C08
82	SA18 ENBAJADA	→	C09
102	SA19 CESA	→	C10
112	SA1A ECOCENTRO	→	C11
132	MODA B1.1-2	→	C12
132	UB B1.1-B1.2	→	C13
152	SA21 TIEMPO AUX	→	C14
162	SA22 ENCANTO AUX	→	C15
172	SA23 BO. POPULAR	→	C17
182	SA24 SALL POPULAR	→	C18
192	SA25 SALL POPULAR	→	C19
202	D2 SIEMENS 40 MVA	→	C20
212	UB B1.2-B1.3	→	C21
212	MEDIA B1.3	→	C22
232	D3 SIEMENS 40 MVA	→	C23
242	SA26 PABLO VI	→	C24
242	SA27 EL GREGO	→	C25
262	SA28 GRANAS	→	C26
272	SA29 EL GREGO	→	C27
282	SA30 ESTACION	→	C28
292	SA31 DC. POLICA	→	C29
312	SA31 DC. POLICA	→	C30
322	SA32 SHERIN AUX	→	C31
332	SA33 TRANSMIEN	→	C32
342	SA34 ESPECIMEN	→	C33
352	SA35 SIEMENS 40 MVA	→	C34
372	SA37 ALAMOS	→	C35
382	SA38 CU. SALT	→	C37
392	SA39 GUAI	→	C38
402	SA3A PETROLERAS	→	C39
412	SA3B GOBERNACION	→	C40

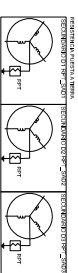

Unidad Organizativa
Administración Información
Técnica Col.

REVISION No. 30
FECHA: AGOSTO/2022
ARCHIVO: SALTRE.DWG
C:\ESQUEMAS SUBESTACIONES\ESQUEMAS DEFINITIVOS

DIAGRAMA UNIFILAR
SUBESTACION SALTRE 2
DIAGONAL 53 N° 68 - 62 (ESQUINA)
SIEMENS 6564
CODIGO: SA

HOJA: 2
DE: 2