


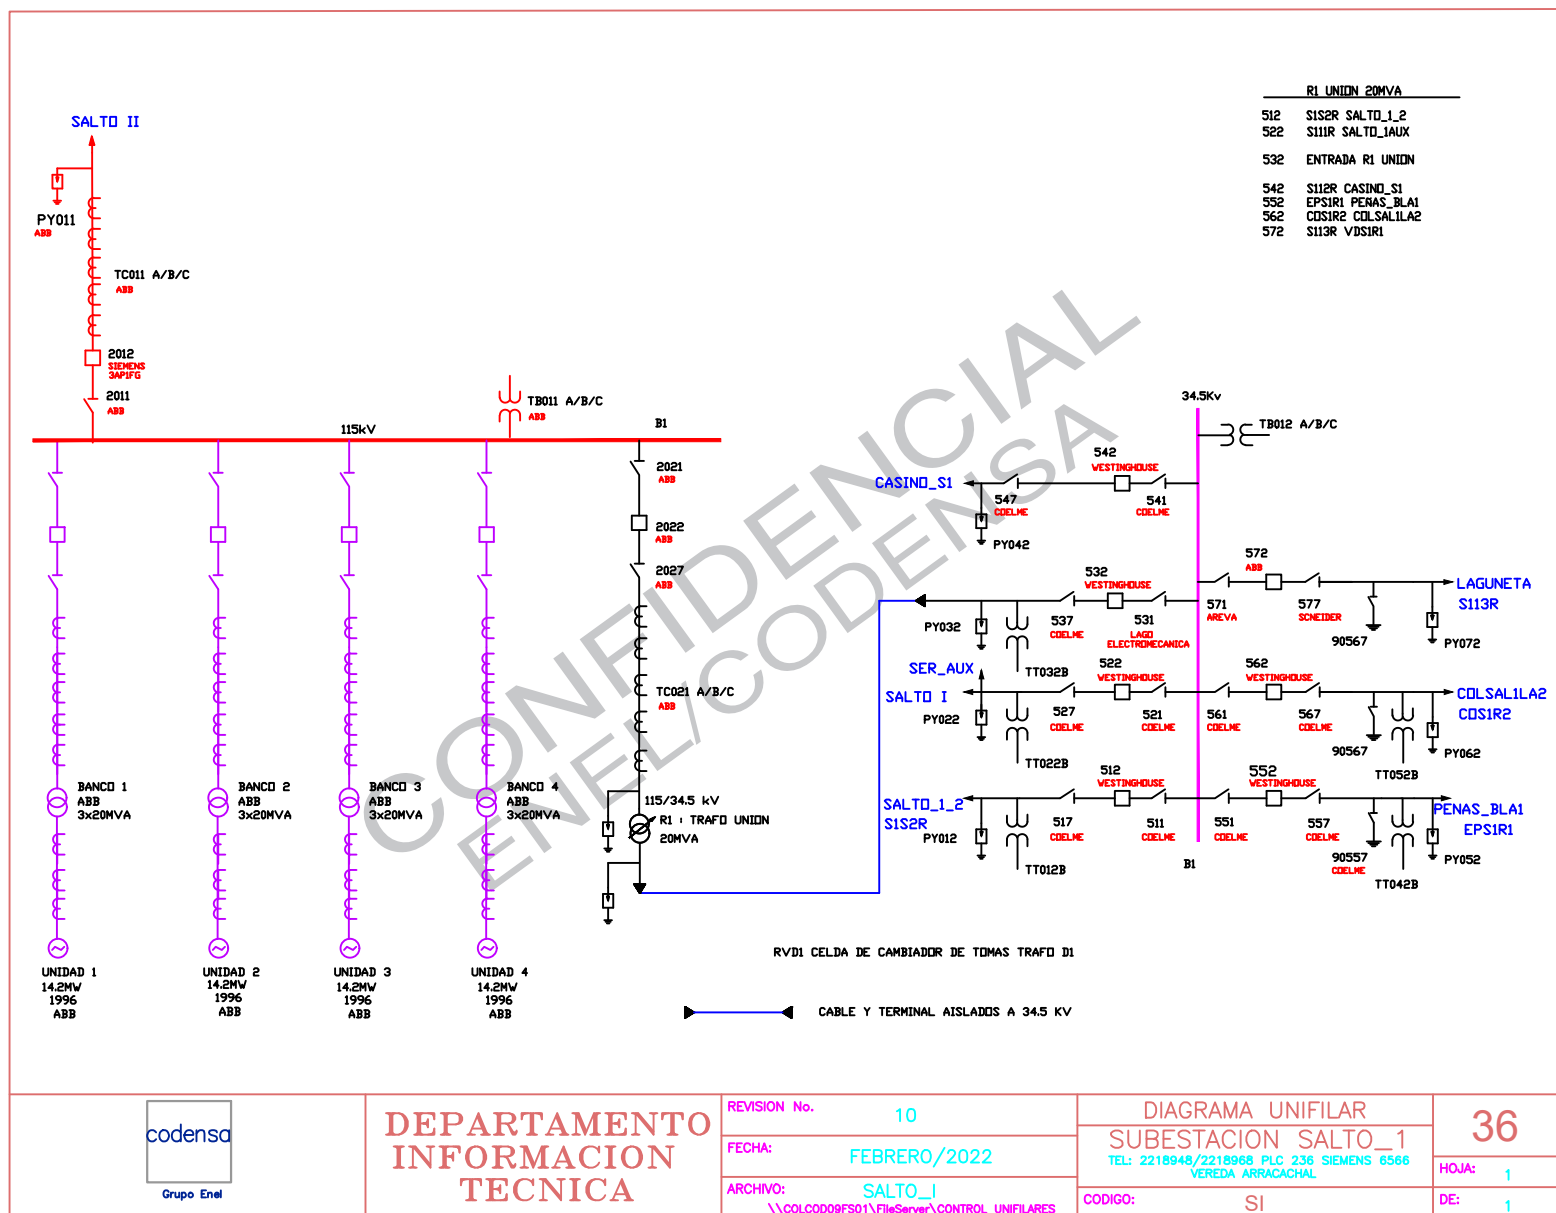

**DEPARTAMENTO
INFORMACION
TECNICA**

REVISION No.	10
FECHA:	FEBRERO/2022
ARCHIVO:	SALTO_I \\COLC0009FS01\FileServer\CONTROL UNIFILARES

DIAGRAMA UNIFILAR	
SUBESTACION SALTO_1	
TEL: 2218948/2218968 PLC 236 SIEMENS 6566	
VEREDA ARRACACHAL	
CODIGO:	SI

36

HOJA:	1
DE:	1