


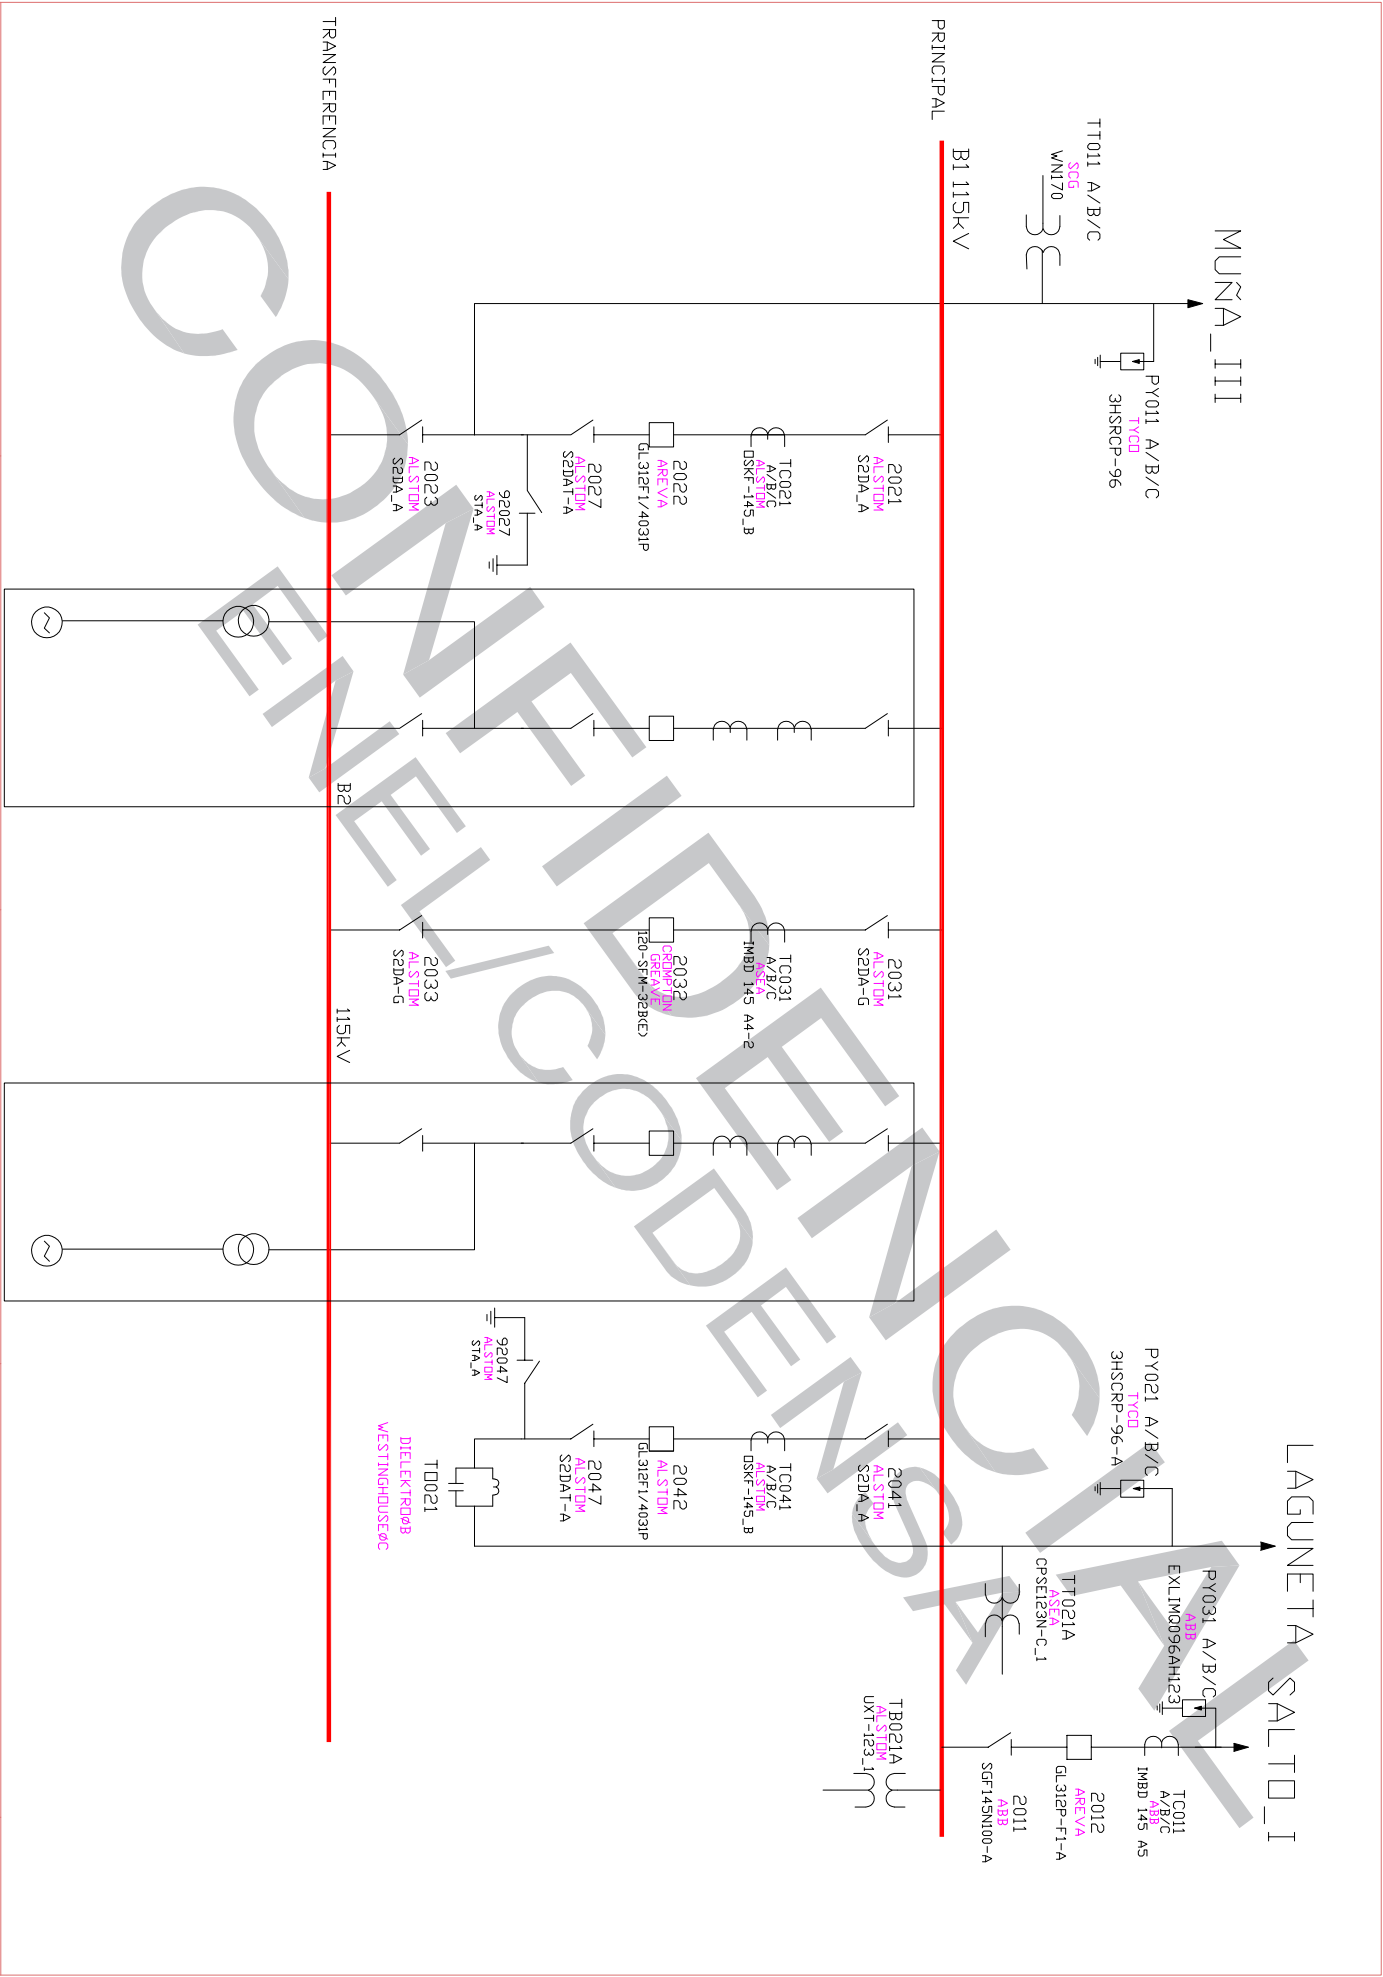

DEPARTAMENTO
INFORMACION
TECNICA

REVISION No.		DIAGRAMA UNIFILAR	
10		37	
FECHA:		SUBESTACION SALTO_II	
MARZO/2019		VEREDA ARRACACHAL	
ARCHIVO:		TEL: 6274600/6531690 PLC237 SIEMENS 6568	
SALTO_II.DWG		HOJA: 1	
\\COLC0009FS01\FilesServer\CONTROL UNIFILARES		CODIGO: S2	
		DE: 1	