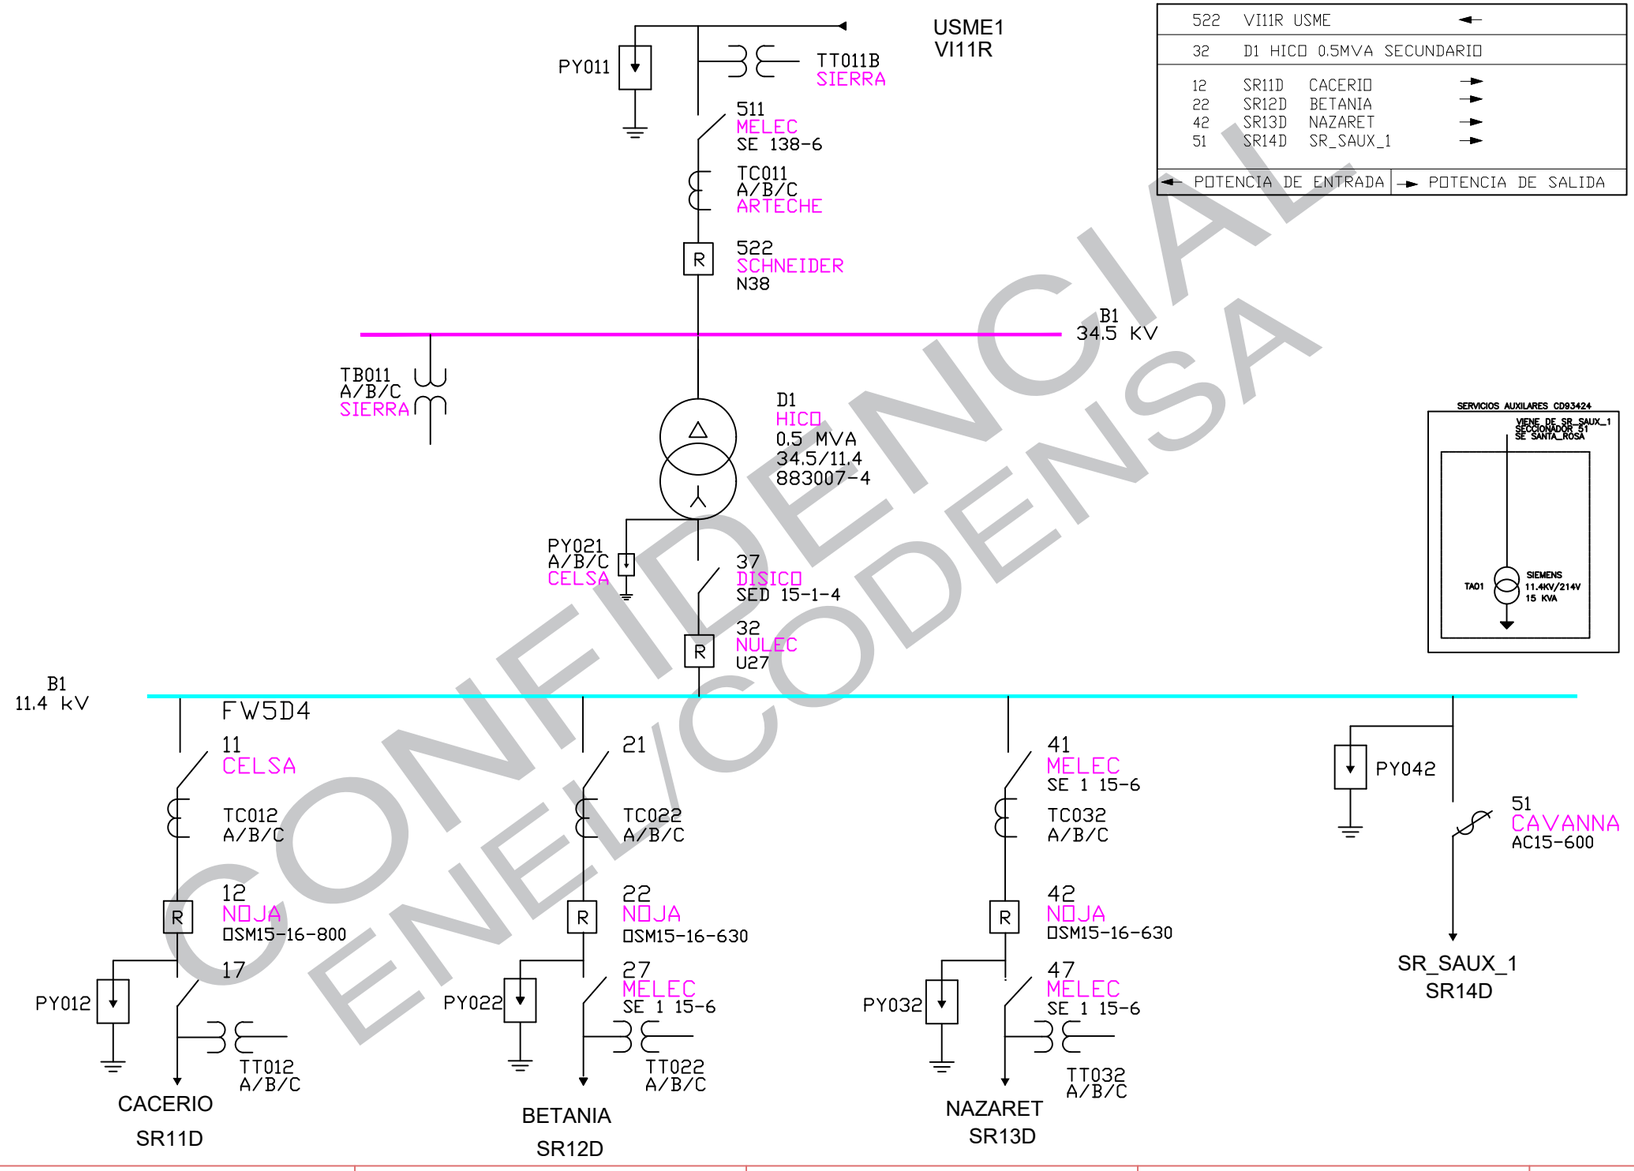

CONFIDENCIAL
ENEL/CODENSA

enel codensa	Unidad Organizativa Administración Información Técnica Col	REVISION No. 8	DIAGRAMA UNIFILAR
		FECHA: ENERO/2022	SUBESTACION SANTA ROSA KM 40 VIA USME SANTA ROSA
		ARCHIVO: SANTA ROSA.DWG C:\ESQUEMAS SUBESTACIONES\ESQUEMAS DEFINITIVOS	CODIGO: SR

77

HOJA: 1

DE: 1