


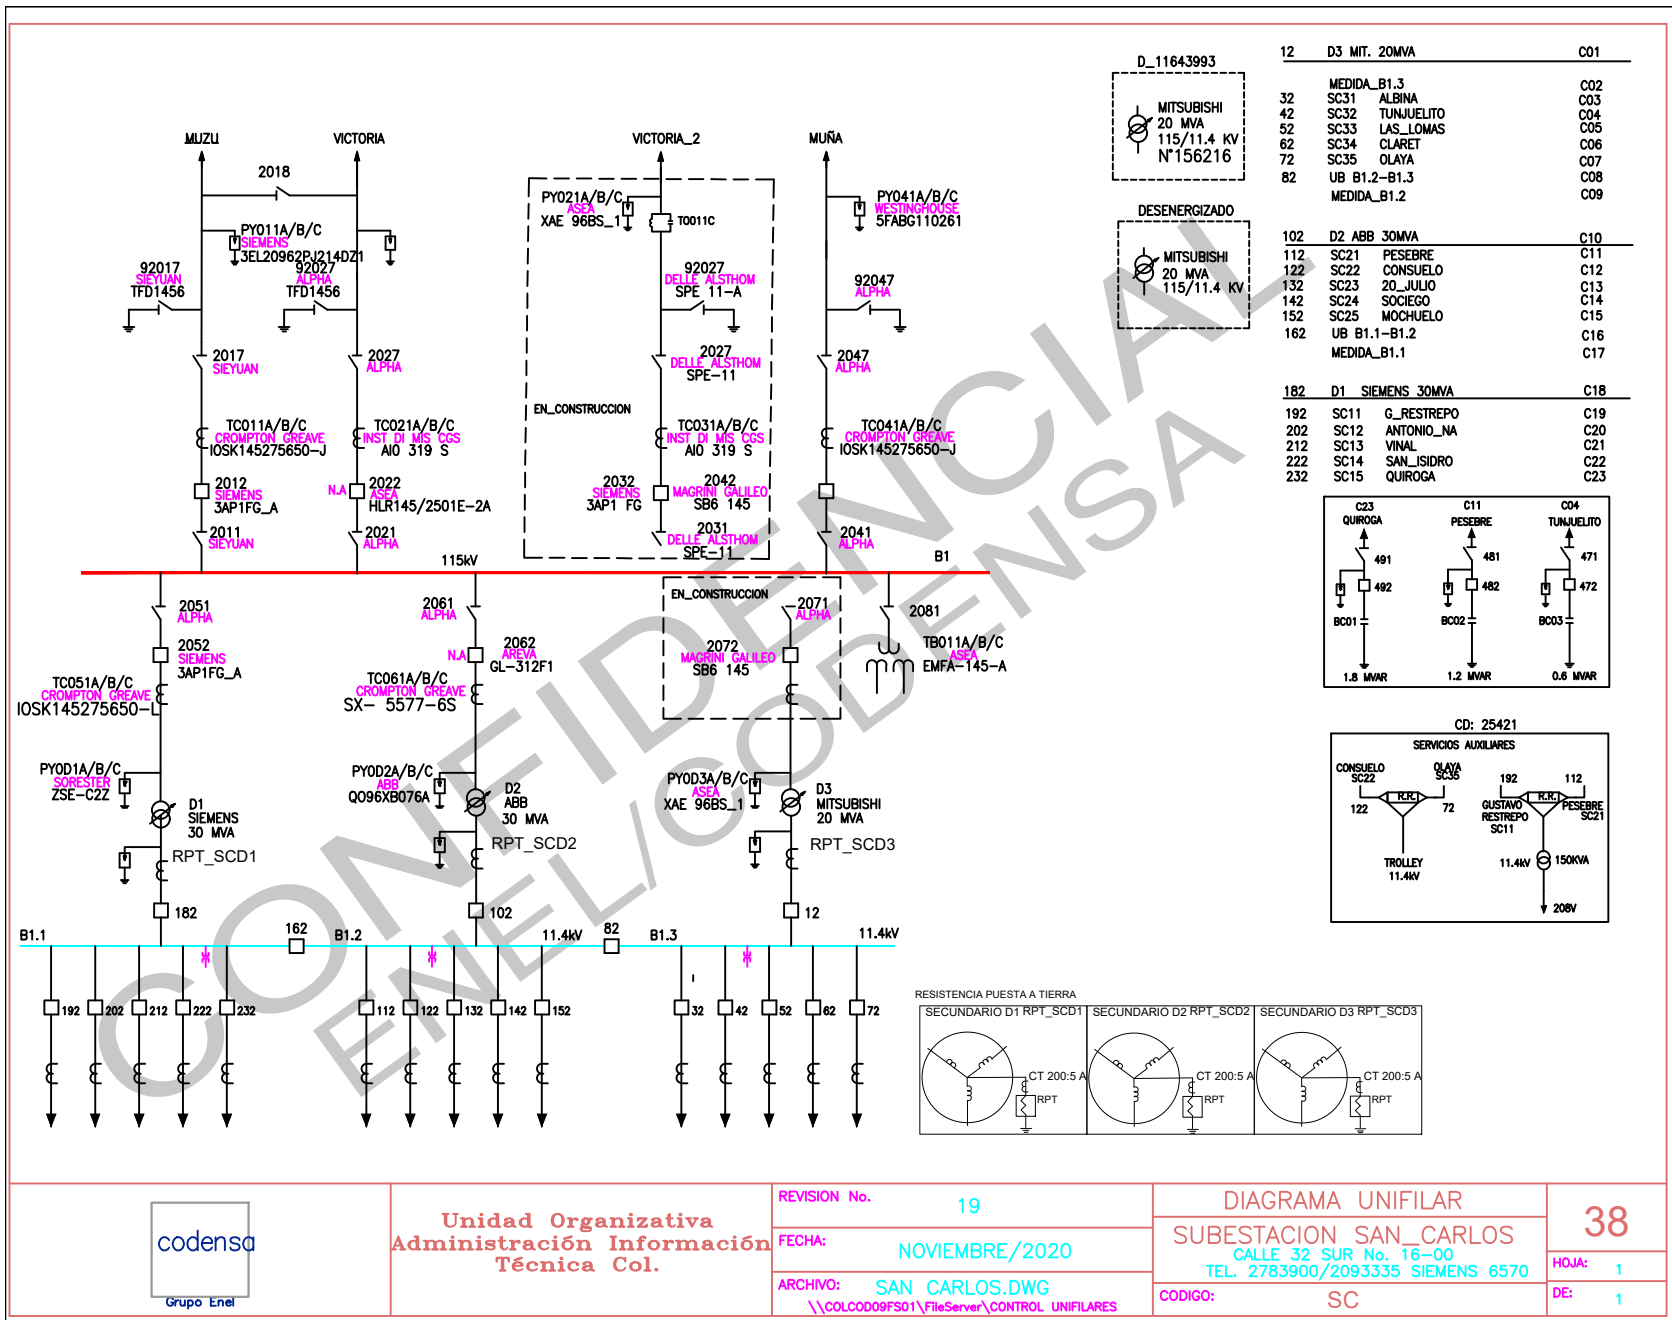

Unidad Organizativa
Administración Información
Técnica Col.

REVISIÓN No.	19
FECHA:	NOVIEMBRE/2020
ARCHIVO:	SAN CARLOS.DWG \\COLCOD09FS01\FileServer\CONTROL UNIFILARES

DIAGRAMA UNIFILAR
SUBESTACION SAN_CARLOS
CALLE 32 SUR No. 16-00
TEL. 2783900/2093335 SIEMENS 6570
CODIGO: SC

38

HOJA: 1
DE: 1