

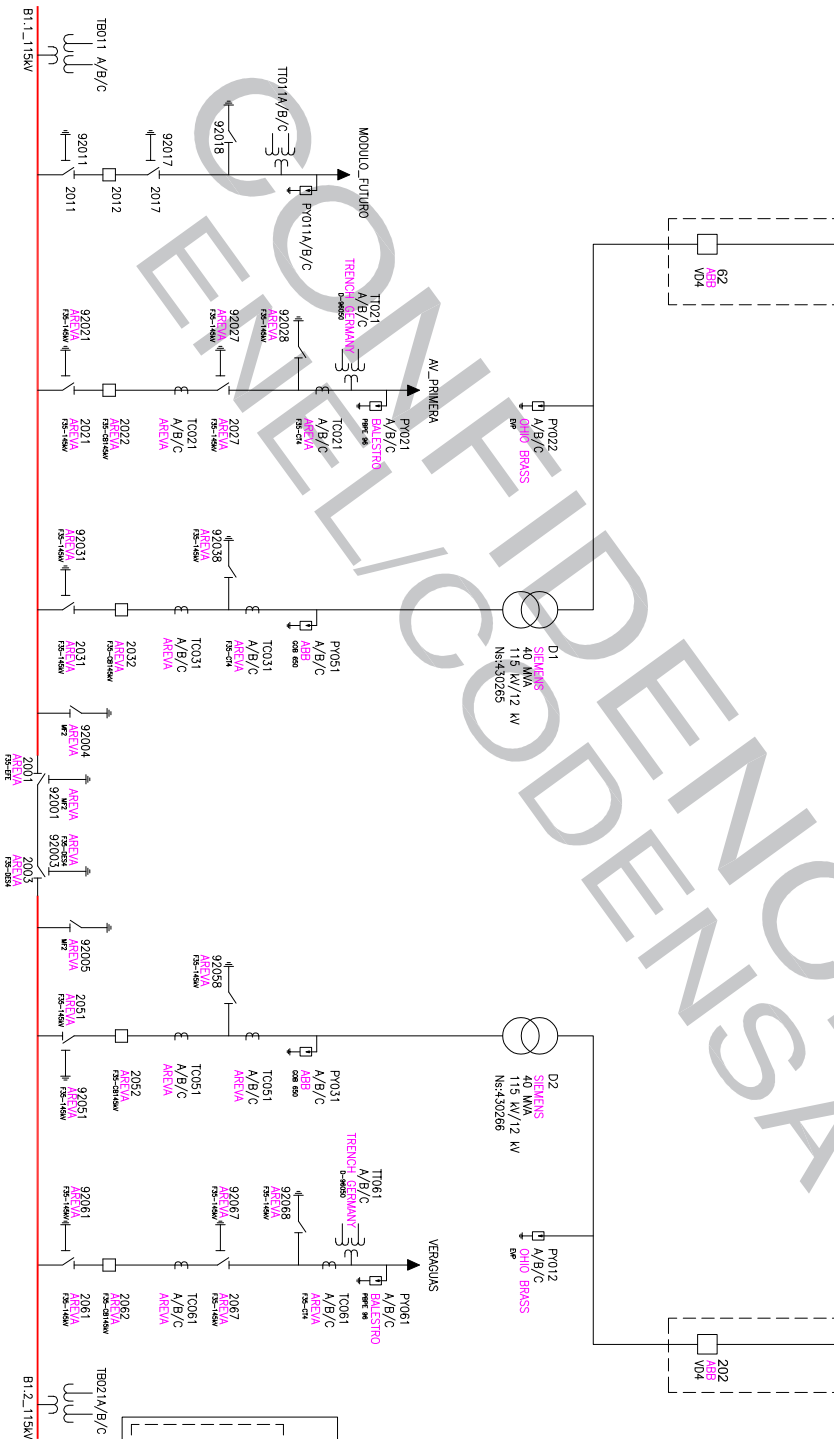


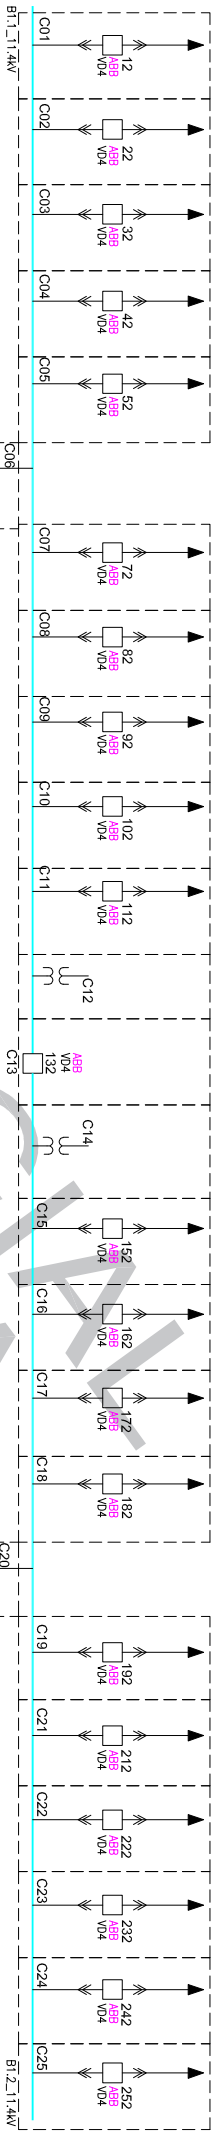

12	SJ11	CU I BOGOTA	C01
22	SJ12	EDU COLON	C02
32	SJ13	CARUCHINA	C03
42	SJ14	EDITORIAL	C04
52	SJ15	ESTANZUELA	C05
62	SJ16	D1 40 MVA SIEMENS	C06
72	SJ17	MILENIO	C07
82	SJ18	ETB MARTIR	C08
92	SJ19	PEPTA	C09
102	SJ19	LIBRE SJ19	C10
112	SJ1A	SJ SAUX 1	C11
122	SJ21	LIBRE SJ21	C12
132	SJ22	LIBRE SJ22	C13
142	SJ23	LIBRE SJ23	C14
152	SJ24	LIBRE SJ24	C15
162	SJ25	LIBRE SJ25	C16
172	SJ26	LIBRE SJ26	C17
182	SJ27	LIBRE SJ27	C18
192	SJ28	LIBRE SJ28	C19
202	SJ29	LIBRE SJ29	C20
212	SJ30	LIBRE SJ30	C21
222	SJ31	LIBRE SJ31	C22
232	SJ32	LIBRE SJ32	C23
242	SJ33	LIBRE SJ33	C24
252	SJ34	LIBRE SJ34	C25

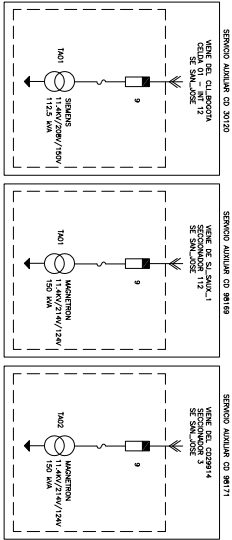

DEPARTAMENTO INFORMACION TECNICA

REVISION No. 19
FECHA: ENERO/2023
ARCHIVO: SAN_JOSE.DWG
\\C03.CODINFORMACION\CONTROL_UNIDADES

DIAGRAMA UNIFILAR
SUBESTACION SAN JOSE
CARRERA 20 No. 11-24
TEL. 2373415/2475015 SIEMENS 6574

CODIGO: SJ
HOLAJA: 1
DE: 1