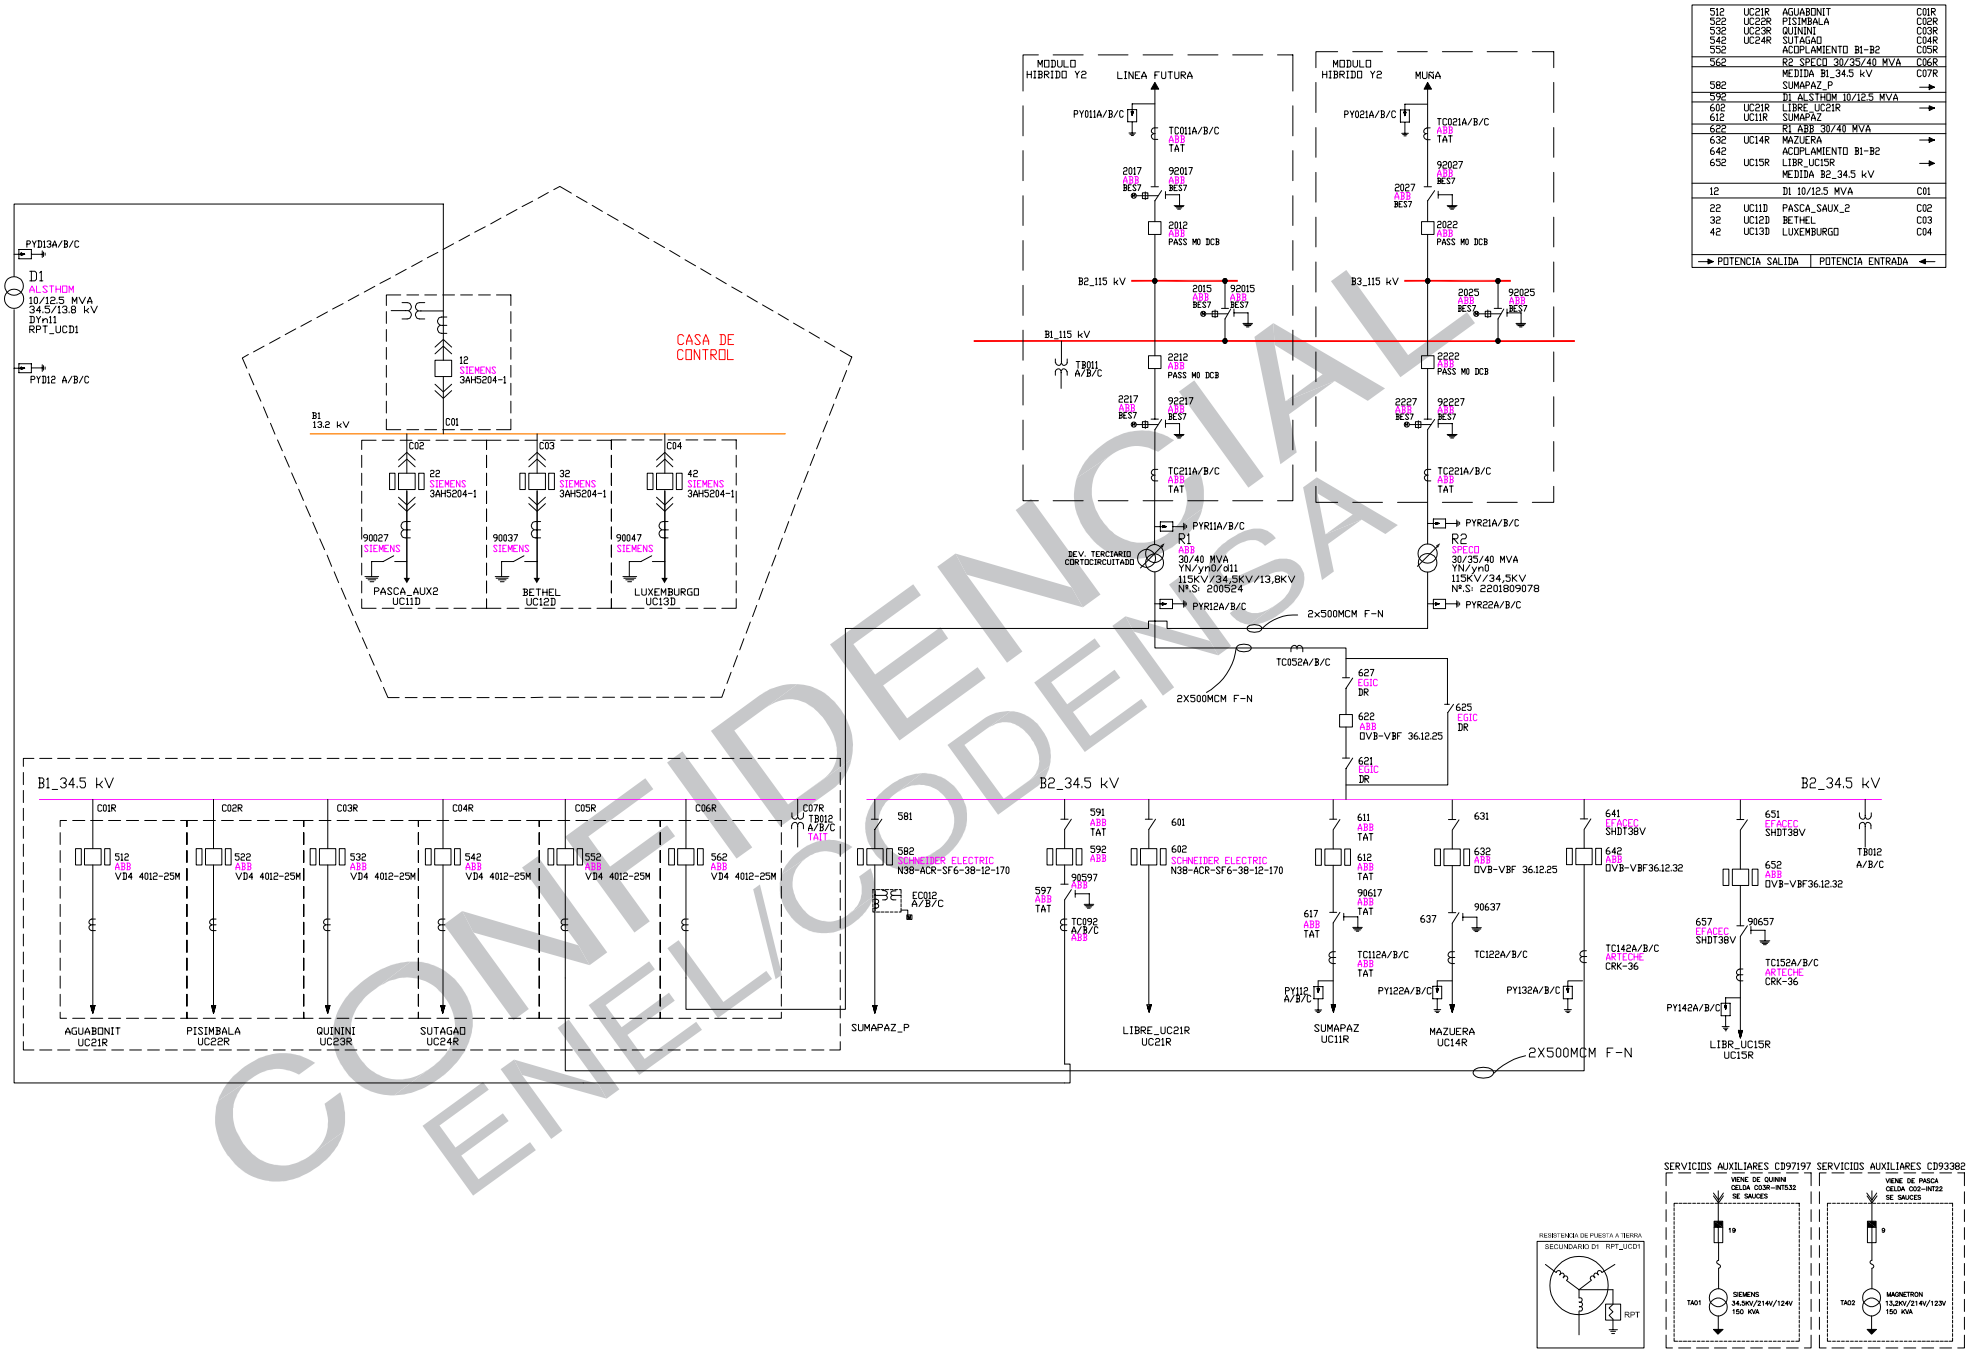


512	UC21R	AGUABONIT	C01R
522	UC22R	PISIMBALA	C02R
532	UC23R	QUININI	C03R
542	UC24R	SUTAGAO	C04R
552		ACOPLAMIENTO B1-B2	C05R
562		R2 SPECO 30/35/40 MVA	C06R
		MEDIDA B1_34.5 kV	C07R
582		SUMAPAZ_P	→
592		D1 ALSTHOM 10/12.5 MVA	
602	UC21R	LIBRE UC21R	→
612	UC11R	SUMAPAZ	→
622		R1 ABB 30/40 MVA	
632	UC14R	MAZUERA	→
642		ACOPLAMIENTO B1-B2	
652	UC15R	LIBR_UC15R	→
		MEDIDA B2_34.5 kV	
12		D1 10/12.5 MVA	C01
22	UC11D	PASCA_AUX_2	C02
32	UC12D	BETHEL	C03
42	UC13D	LUXEMBURGO	C04

→ POTENCIA SALIDA | POTENCIA ENTRADA ←

CONFIDENCIAL ENEL CODENSA

enel codensa	Unidad Organizativa Administraciòn Informaciòn Tècnica Col	REVISION No. 21	DIAGRAMA UNIFILAR
		FECHA: ENERO/2023	SUBESTACION SAUCES
		ARCHIVO: SAUCES.DWG Y:\FileServer\CONTROL UNIFILARES\	MUNICIPIO DE GIRARDOT
		CODIGO: UC	77
			HOJA: 1
			DE: 1