


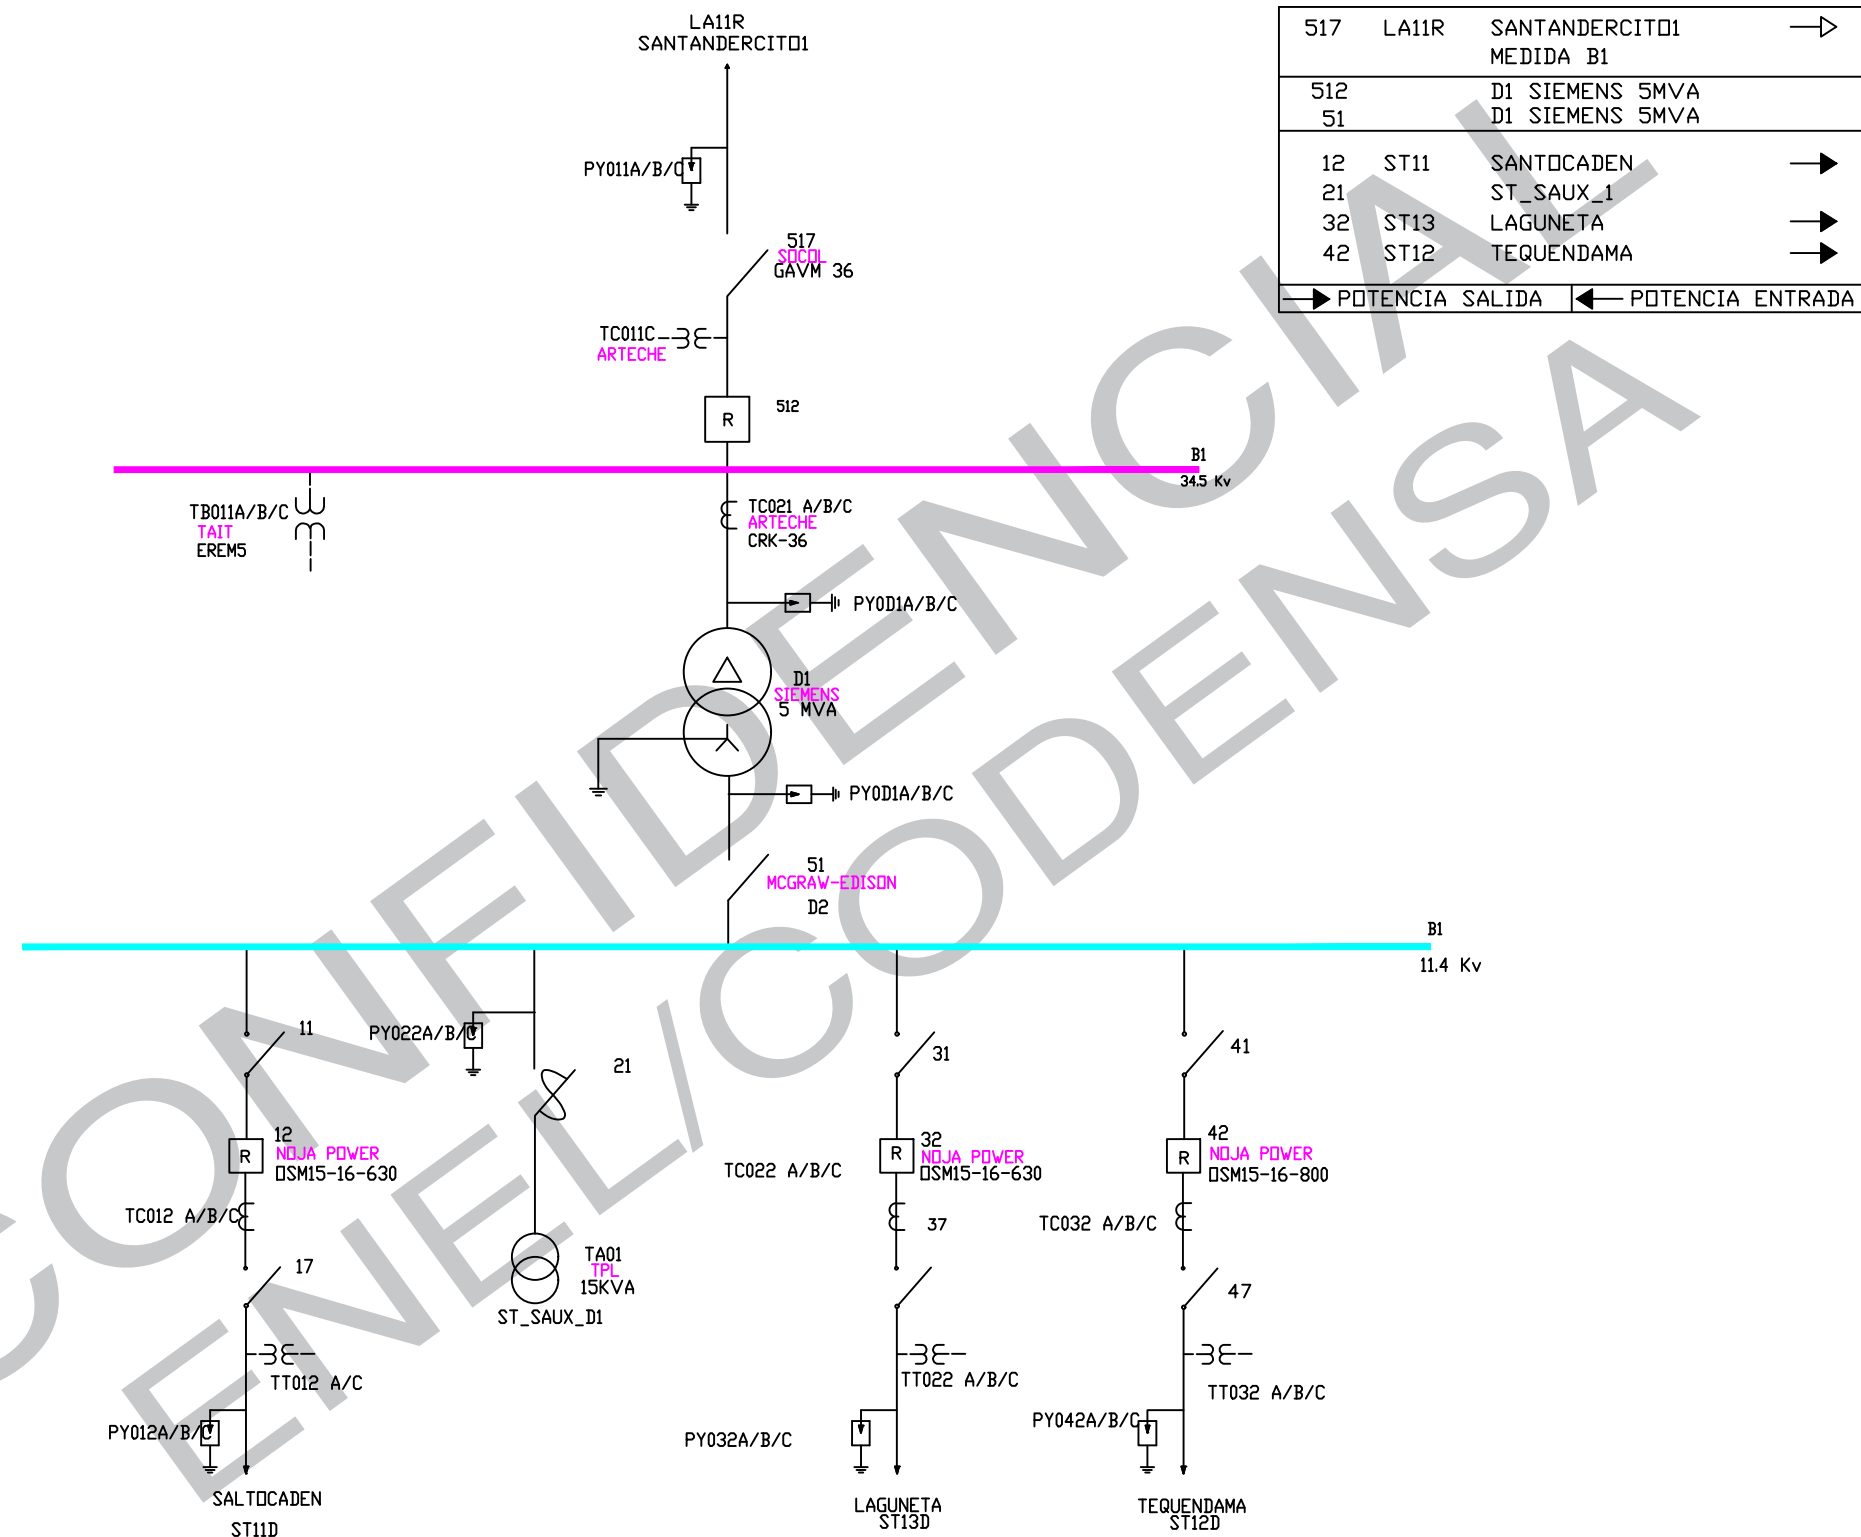

Unidad Organizativa
Administración Información
Técnica Col

REVISION No. 14
FECHA: ENERO/2022
ARCHIVO: SANTANDERCITO.DWG
\\COLCOD09FS01\FileServer\CONTROL UNIFILARES

DIAGRAMA UNIFILAR
SUBESTACION SANTANDERCITO
M/PIO SANTANDERCITO VIA EL PROGRESO
CODIGO: ST

105

HOJA: 1
DE: 1