

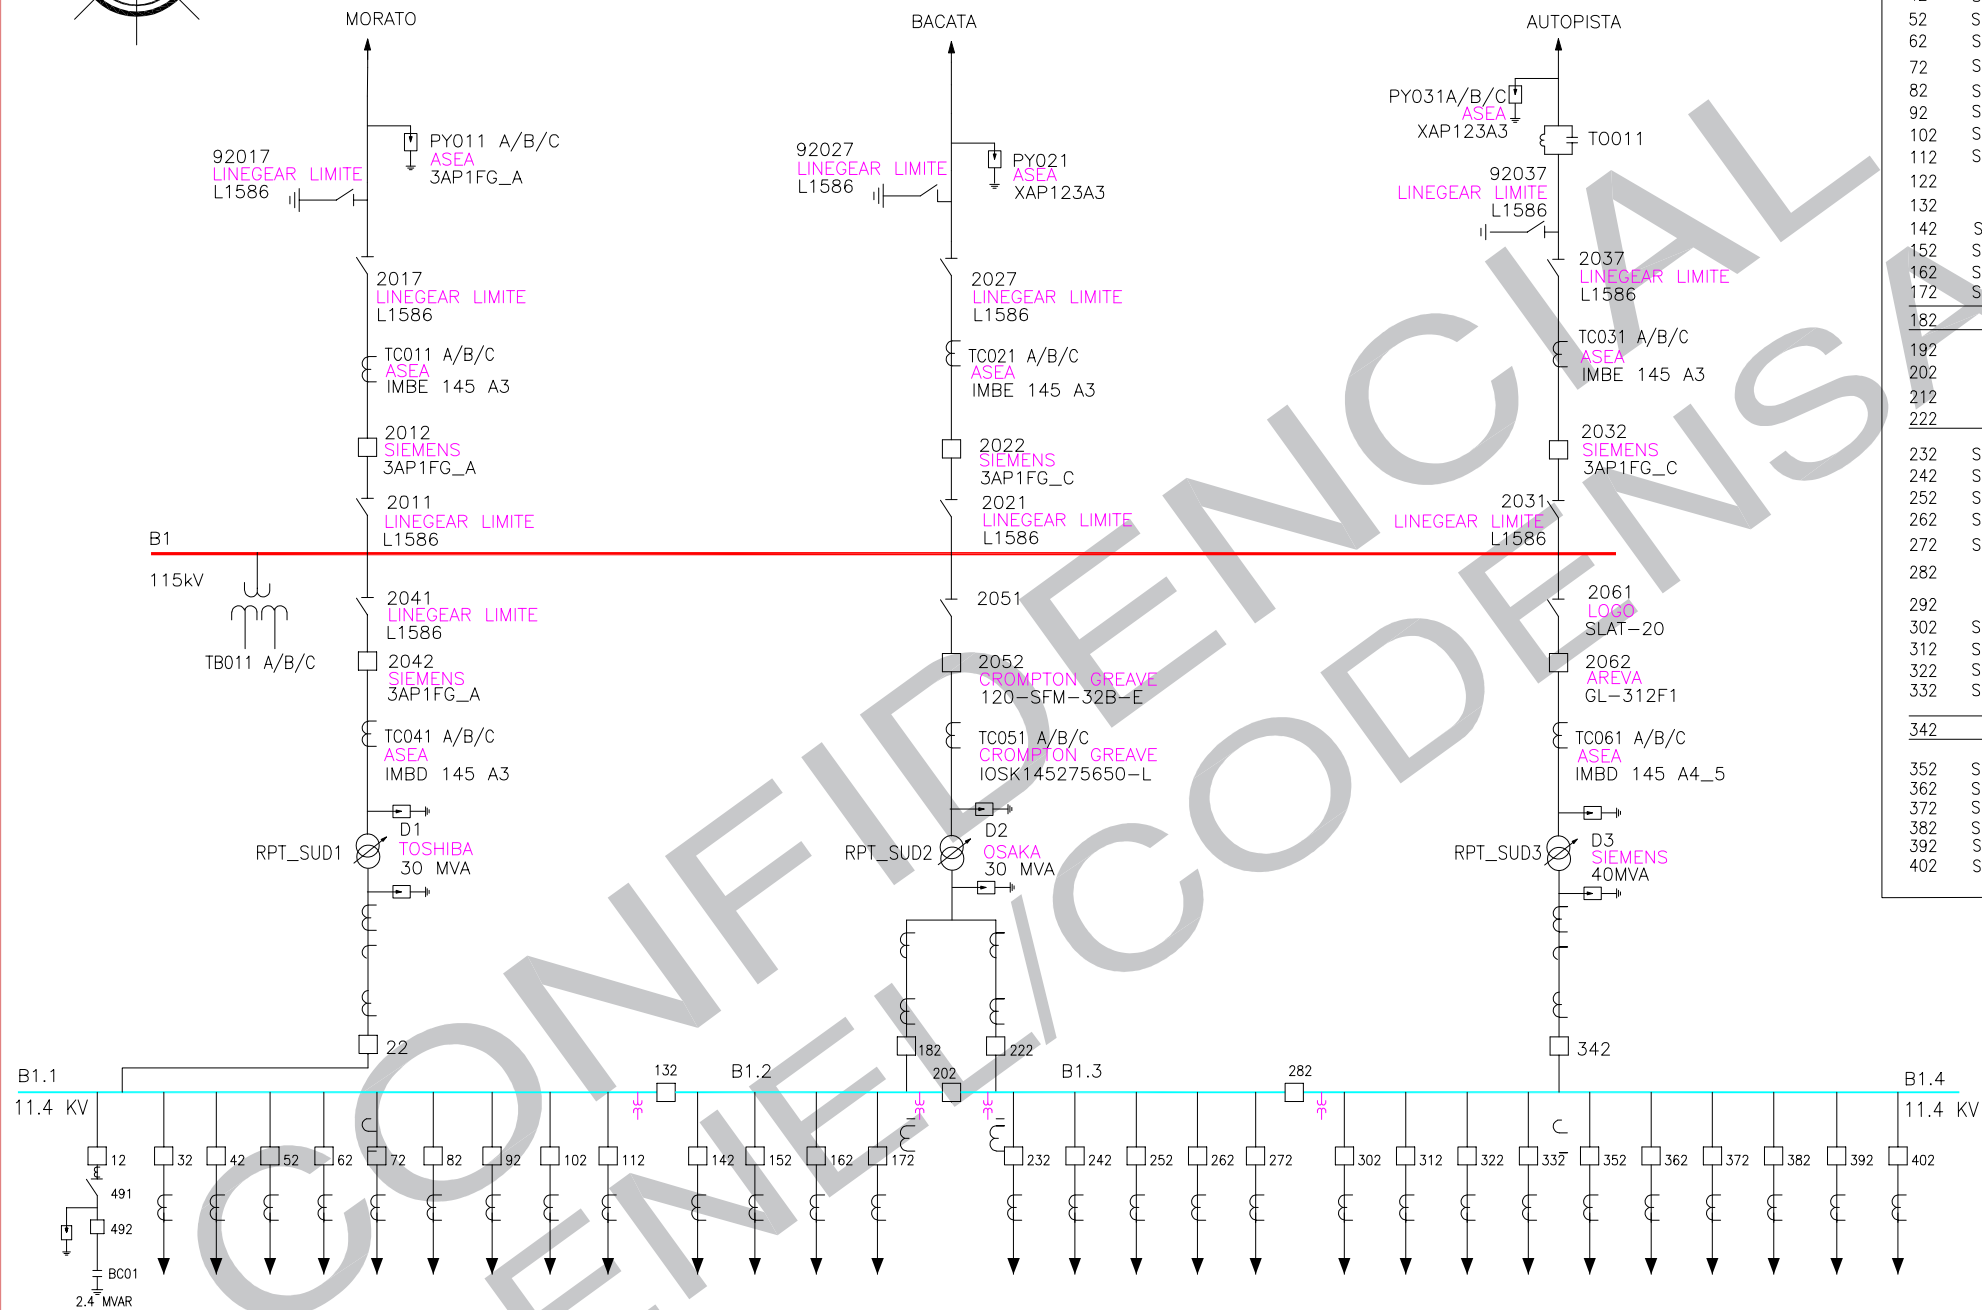
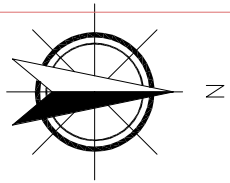
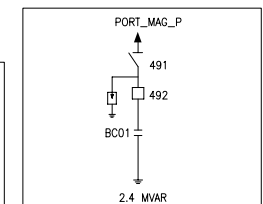


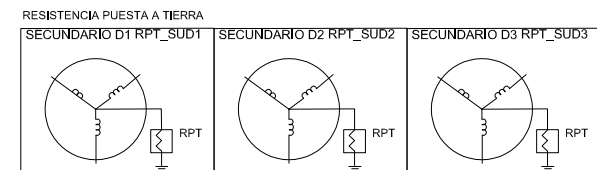

12	SU1A	CONEJERA	C01
22	D1	TOSHIBA 30MVA	C02
32	SU11	MAZUREN	C03
42	SU12	PROVENZA	C04
52	SU13	VL_MAGDALA	C05
62	SU14	TERRAVISTA	C06
72	SU15	CAMPANELA	C07
82	SU16	PARCELACIO	C08
92	SU17	VELEZ	C09
102	SU18	ARCADIA	C10
112	SU19	TOLU	C11
122		MEDIDA BARRA 1.1	C12
132		UNION BARRAS 1.1/1.2	C13
142	SU21	BACATA	C14
152	SU22	PORTALES	C15
162	SU23	BOSTON	C16
172	SU24	VL_PRADO	C17
182		D2 OSAKA 30MVA	C18
192		MEDIDA 1.1	C19
202		UNION BARRAS 1.2/1.3	C20
212		MEDIDA 1.3	C21
222		D2 OSAKA 30MVA	C22
232	SU25	LA SIRENA	C23
242	SU26	MULTIDRIVE	C24
252	SU27	TOSCANA	C25
262	SU28	POPAYAN	C26
272	SU29	CALAZANS	C27
282		UNION BARRAS 1.3/1.4	C28
292		MEDIDA	C29
302	SU31	CARMEN	C30
312	SU32	J_N_CORPAS	C31
322	SU33	CERRITO	C32
332	SU34	BUCARO	C33
342		D3 SIEMENS 40MVA	C34
352	SU35	S_CIPRIANO	C35
362	SU36	LA_CAMPINA	C36
372	SU37	S_MONICA	C37
382	SU38	LINCOLN	C38
392	SU39	CALLE_170	C39
402	SU3A	MUISCA	C40

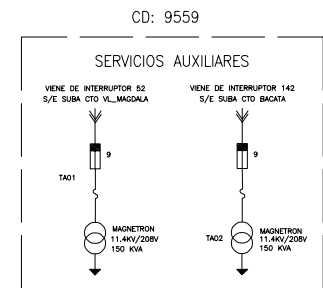

Unidad Organizativa
Administración Información
Técnica Col.

REVISION No. 22

FECHA: JUNIO/2022

ARCHIVO: SUBA.DWG

Y:\FileServer\CONTROL UNIFILARES\UNIFILARES_MARZO_2019

DIAGRAMA UNIFILAR

SUBESTACION SUBA

CARRERA74A N°169A-91
TEL. 6718652/6718592 SIEMENS 6578

CODIGO: SU

47

HOJA: 1

DE: 1