


512	TU21R4	CARRASQUILLA4	C01R
522	TU21R5	CARRASQUILLA5	C02R
532		D1 ABB 5MVA	C03R
542		D2 2.5MVA TPL	C04R
542		D3 2.5MVA TPL	C05R
		MEDIDA_B1	
12	SH13	S_AUX_SH	C01
22	SH12	TABLAZO	C02
32	SH11	PRADERA	C03
42		D1 ABB 5MVA	C04
		MEDIDA_B1.1	C05
62		UB B1.1_B1.2	C06
		MEDIDA_B1.2	C07
82		D2-D3 TPL 2.5MVA	C08
92	SH22	CANICA	C09
102	SH21	LA_YEGUERA	C10
112	SH23	LA_CUESTA	C11

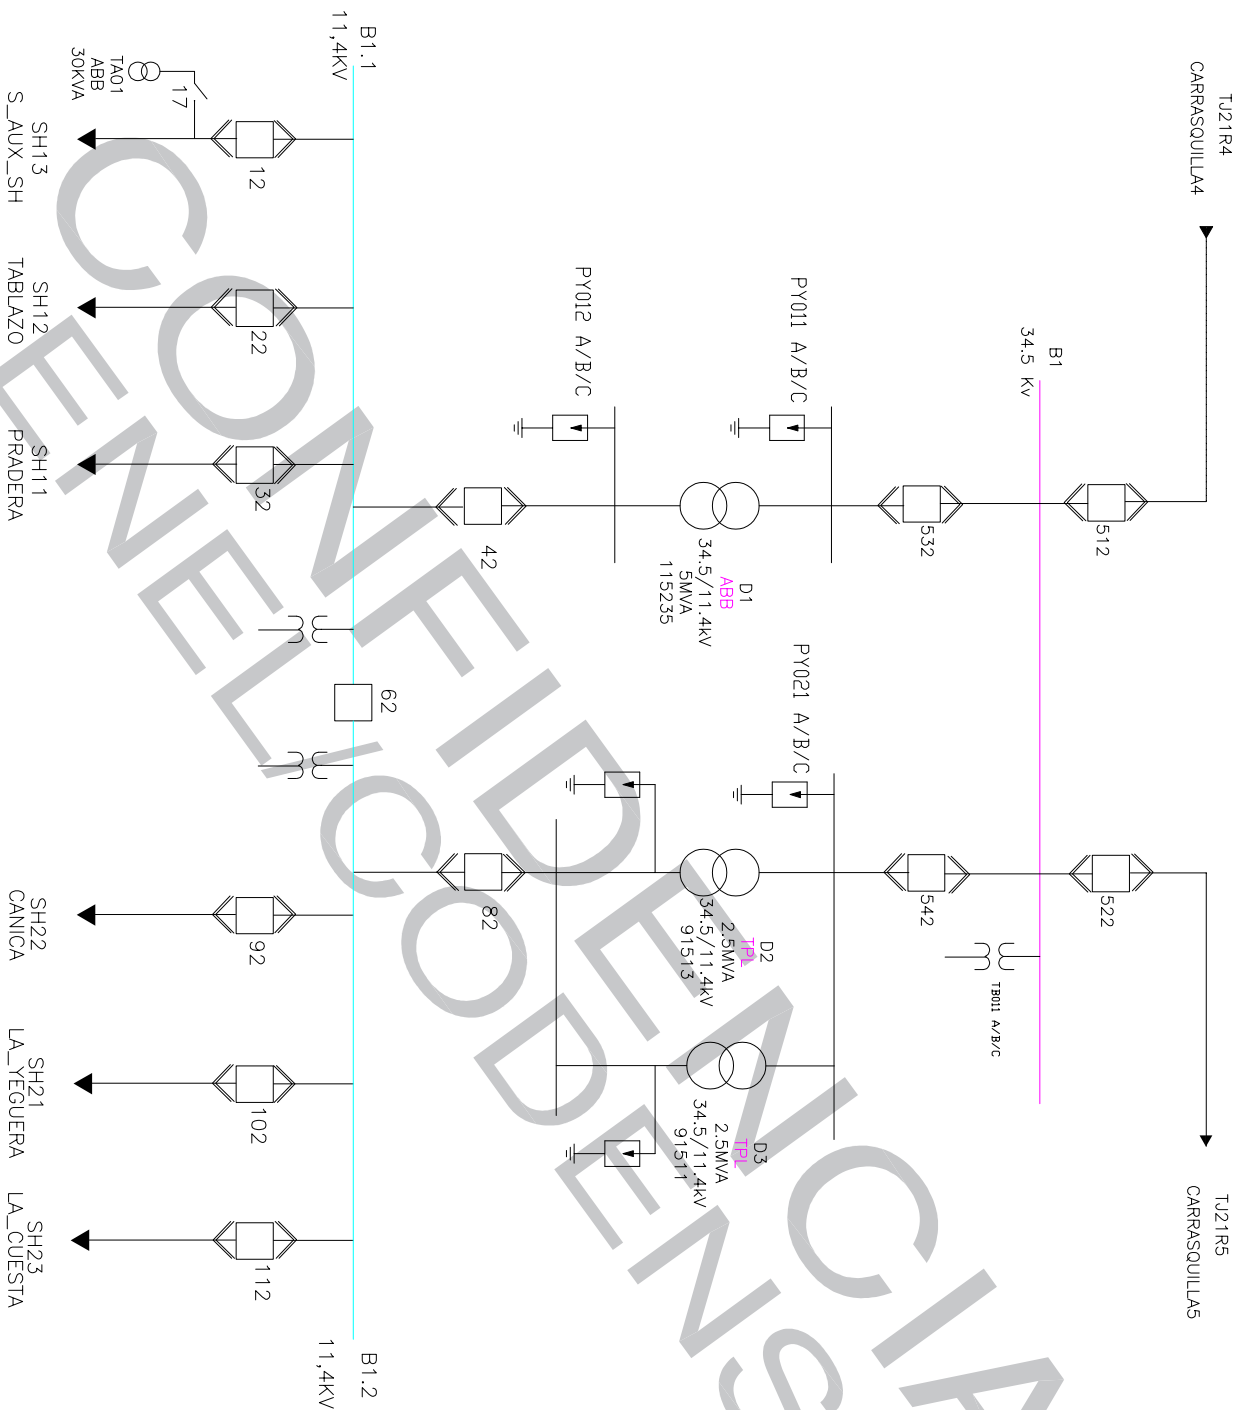

Unidad Organizativa
Administración Informática
Técnica Col.

REVISIÓN No.

8

FECHA: OCTUBRE/2022

ARCHIVO: SUBACHOQUE.DWG

C:\ESQUEMAS SUBESTACIONES\ESQUEMAS DEFINITIVOS

DIAGRAMA UNIFILAR

SUBESTACIÓN SUBACHOQUE

CALE 5 N° 2-11

CODIGO:

SH

HOJA:

1

DE:

1

106