
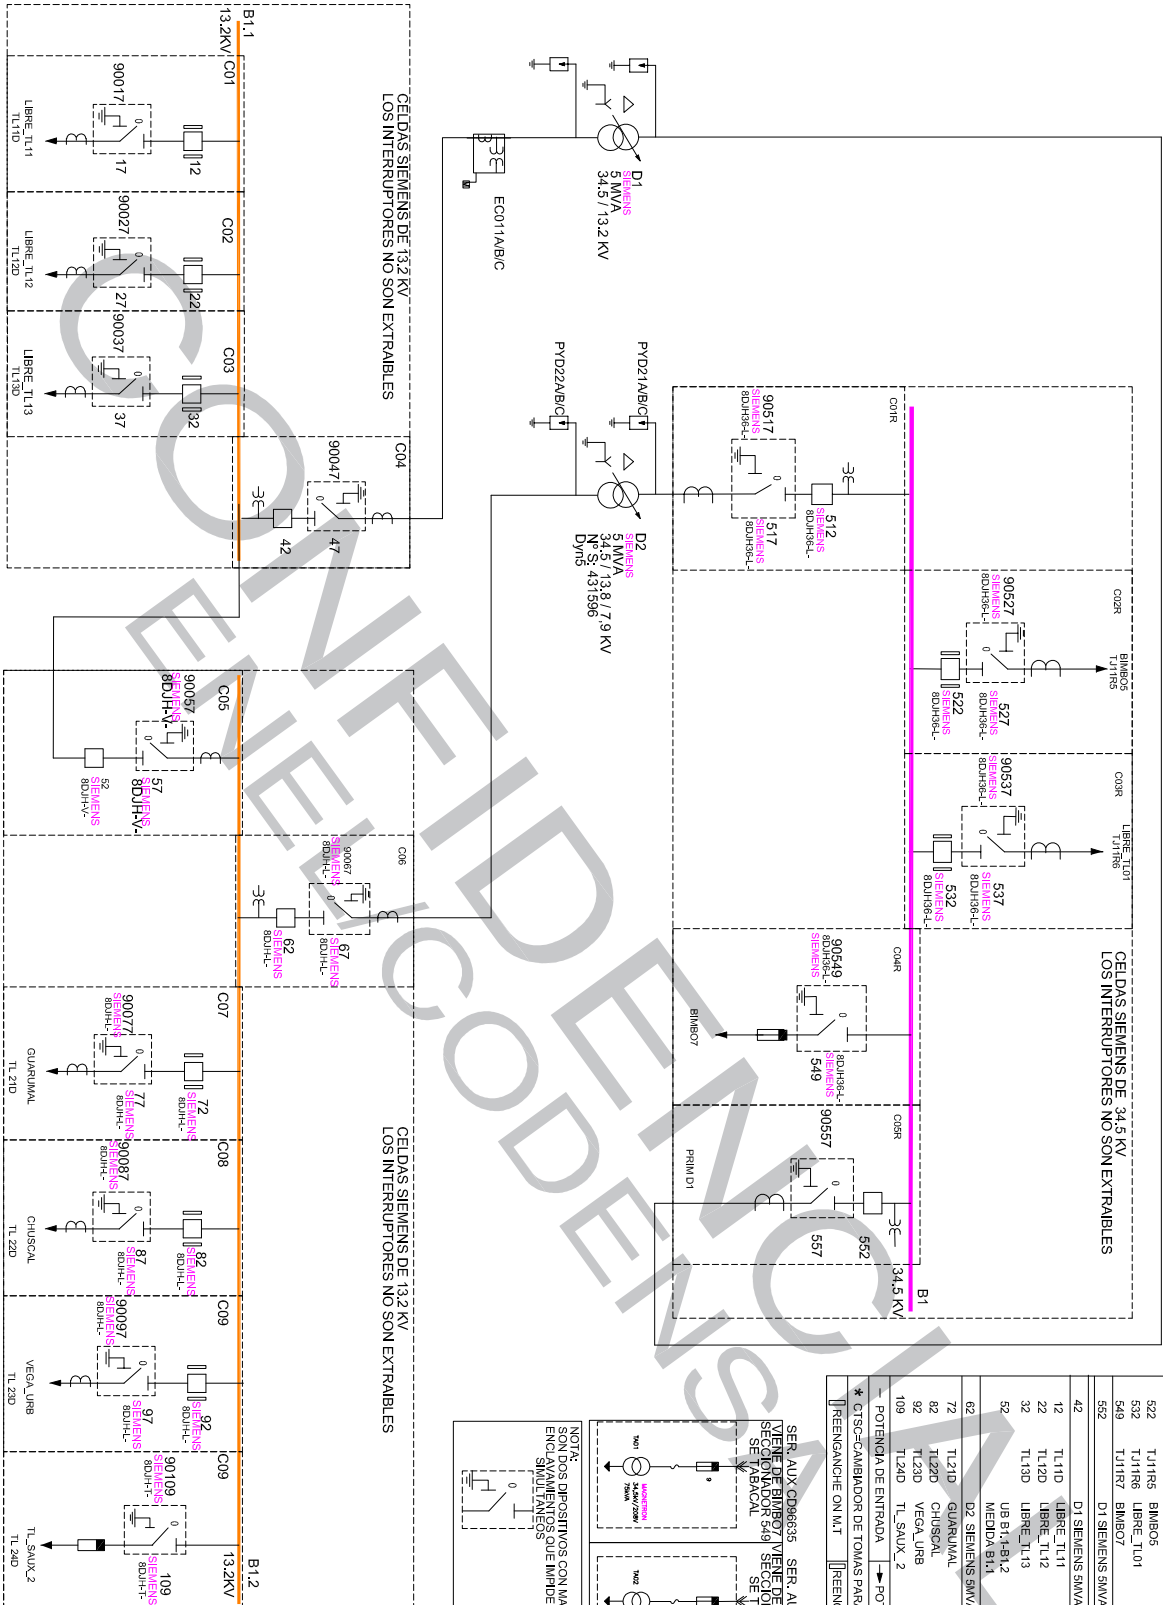
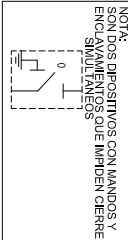


MEDIDA B1.1			
512	D2 SIEMENS 5MVA	→	C01R
522	T11R5 BIMB05	→	C02R
532	T11R6 LIBRE TL101	→	C03R
540	T11R7 BIMB07	→	C04R
552	D1 SIEMENS 5MVA	→	C05R
MEDIDA B1.1			
42	D1 SIEMENS 5MVA	→	C04
12	TL11D LIBRE TL11	→	C01
22	TL12D LIBRE TL12	→	C02
32	TL13D LIBRE TL13	→	C03
52	UB B1.1B12	→	C05
MEDIDA B1.1			
62	D2 SIEMENS 5MVA	→	C06
72	TL21D GUARUMAL	→	C07
82	TL22D CHUSCAL	→	C08
92	VEGA_URB	→	C09
109	TL24D TL_SAVUX_2	→	C10
POTENCIA DE ENTRADA → POTENCIA DE SALIDA			
* CTSC=CAMBIADOR DE TOMAS PARA OPERAR SIN CARGA			
REINTEGRANCHE ON M.T		REINTEGRANCHE ON A.T	

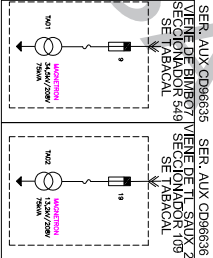

Unidad Organizativa
Administración Informática
Técnica Col.

REVISION No.	6	DIAGRAMA UNIFILAR	238
FECHA:	DICIEMBRE/2022	SUBESTACIÓN TABACAL	
ARCHIVO:	TABACAL.DWG	CODIGO:	TL
HOJA:	1	DE:	1