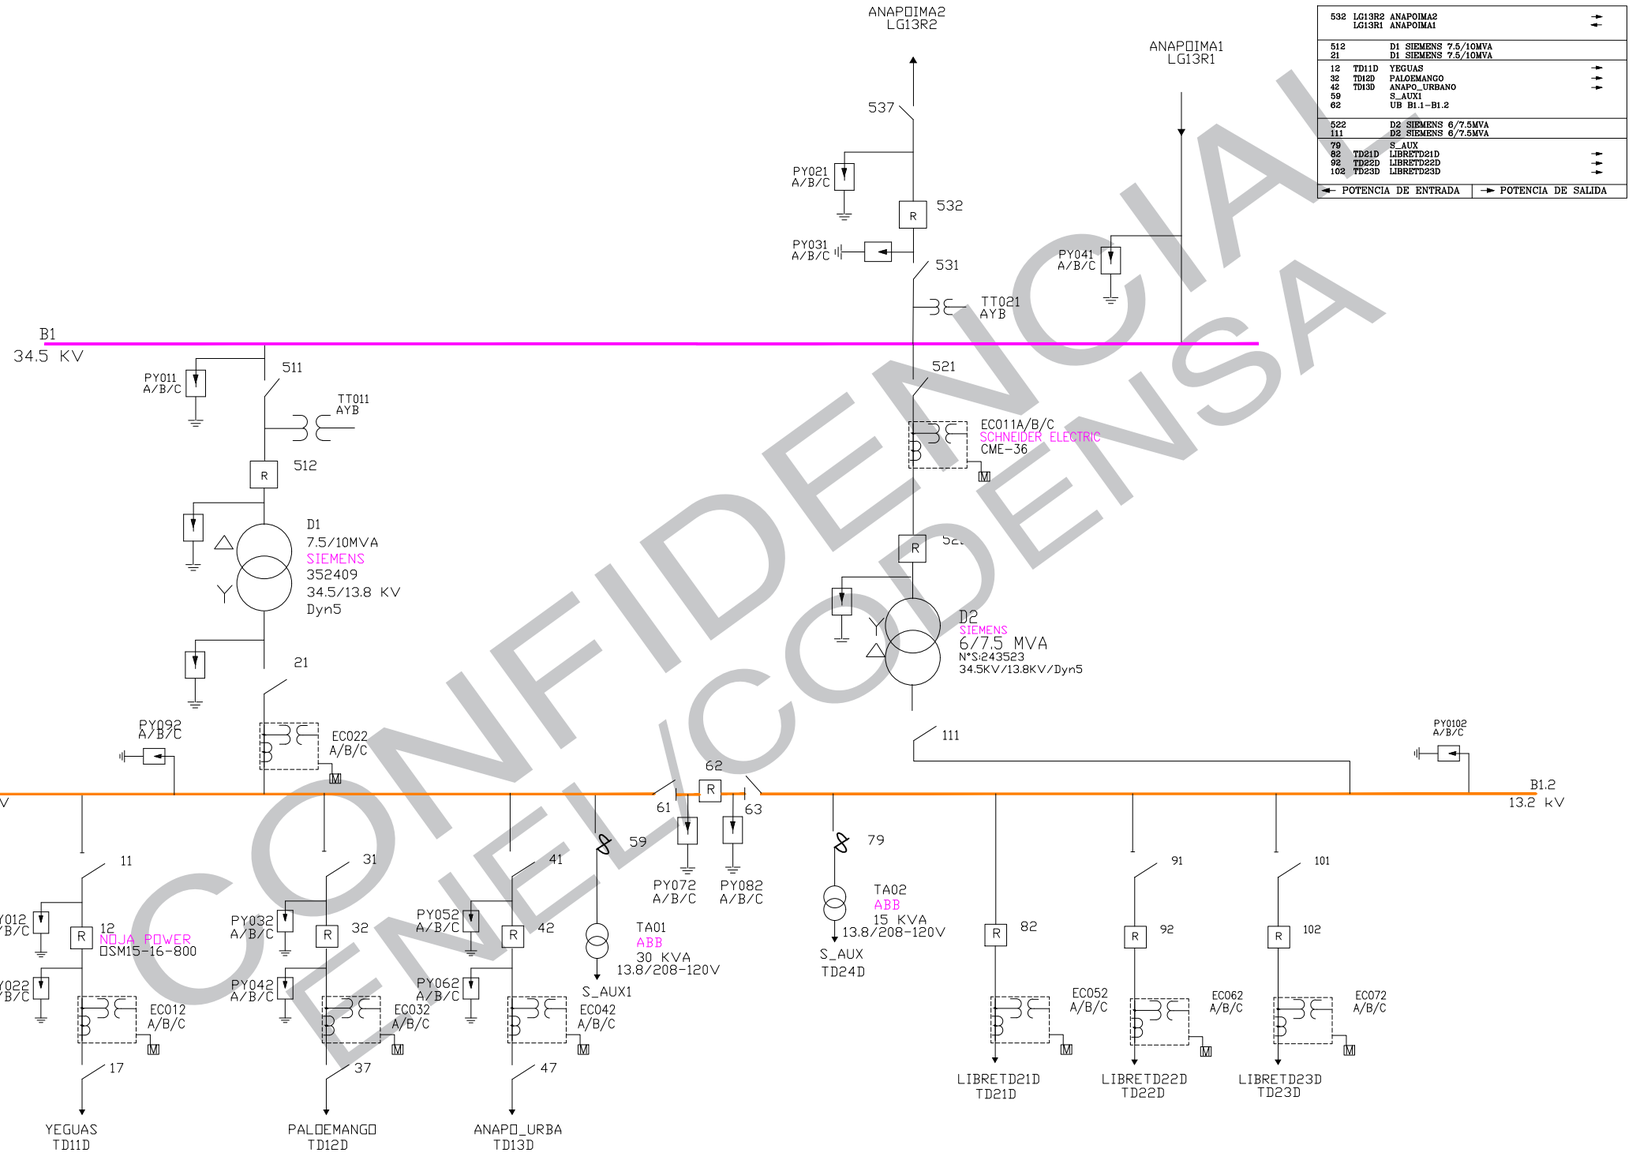


CONFIDENCIAL
ENEL CODENSA

enel codensa	Unidad Organizativa Administración Información Técnica Col	REVISION No. 5 FECHA: MARZO/2022 ARCHIVO: TAMARINDO.DWG C:\ESQUEMAS SUBESTACIONES\ESQUEMAS DEFINITIVOS	DIAGRAMA UNIFILAR SUBESTACION TAMARINDO ANTIGUO ANAPOIMA MUNICIPIO DE ANAPOIMA CODIGO: TD

626

HOJA: 1

DE: 1