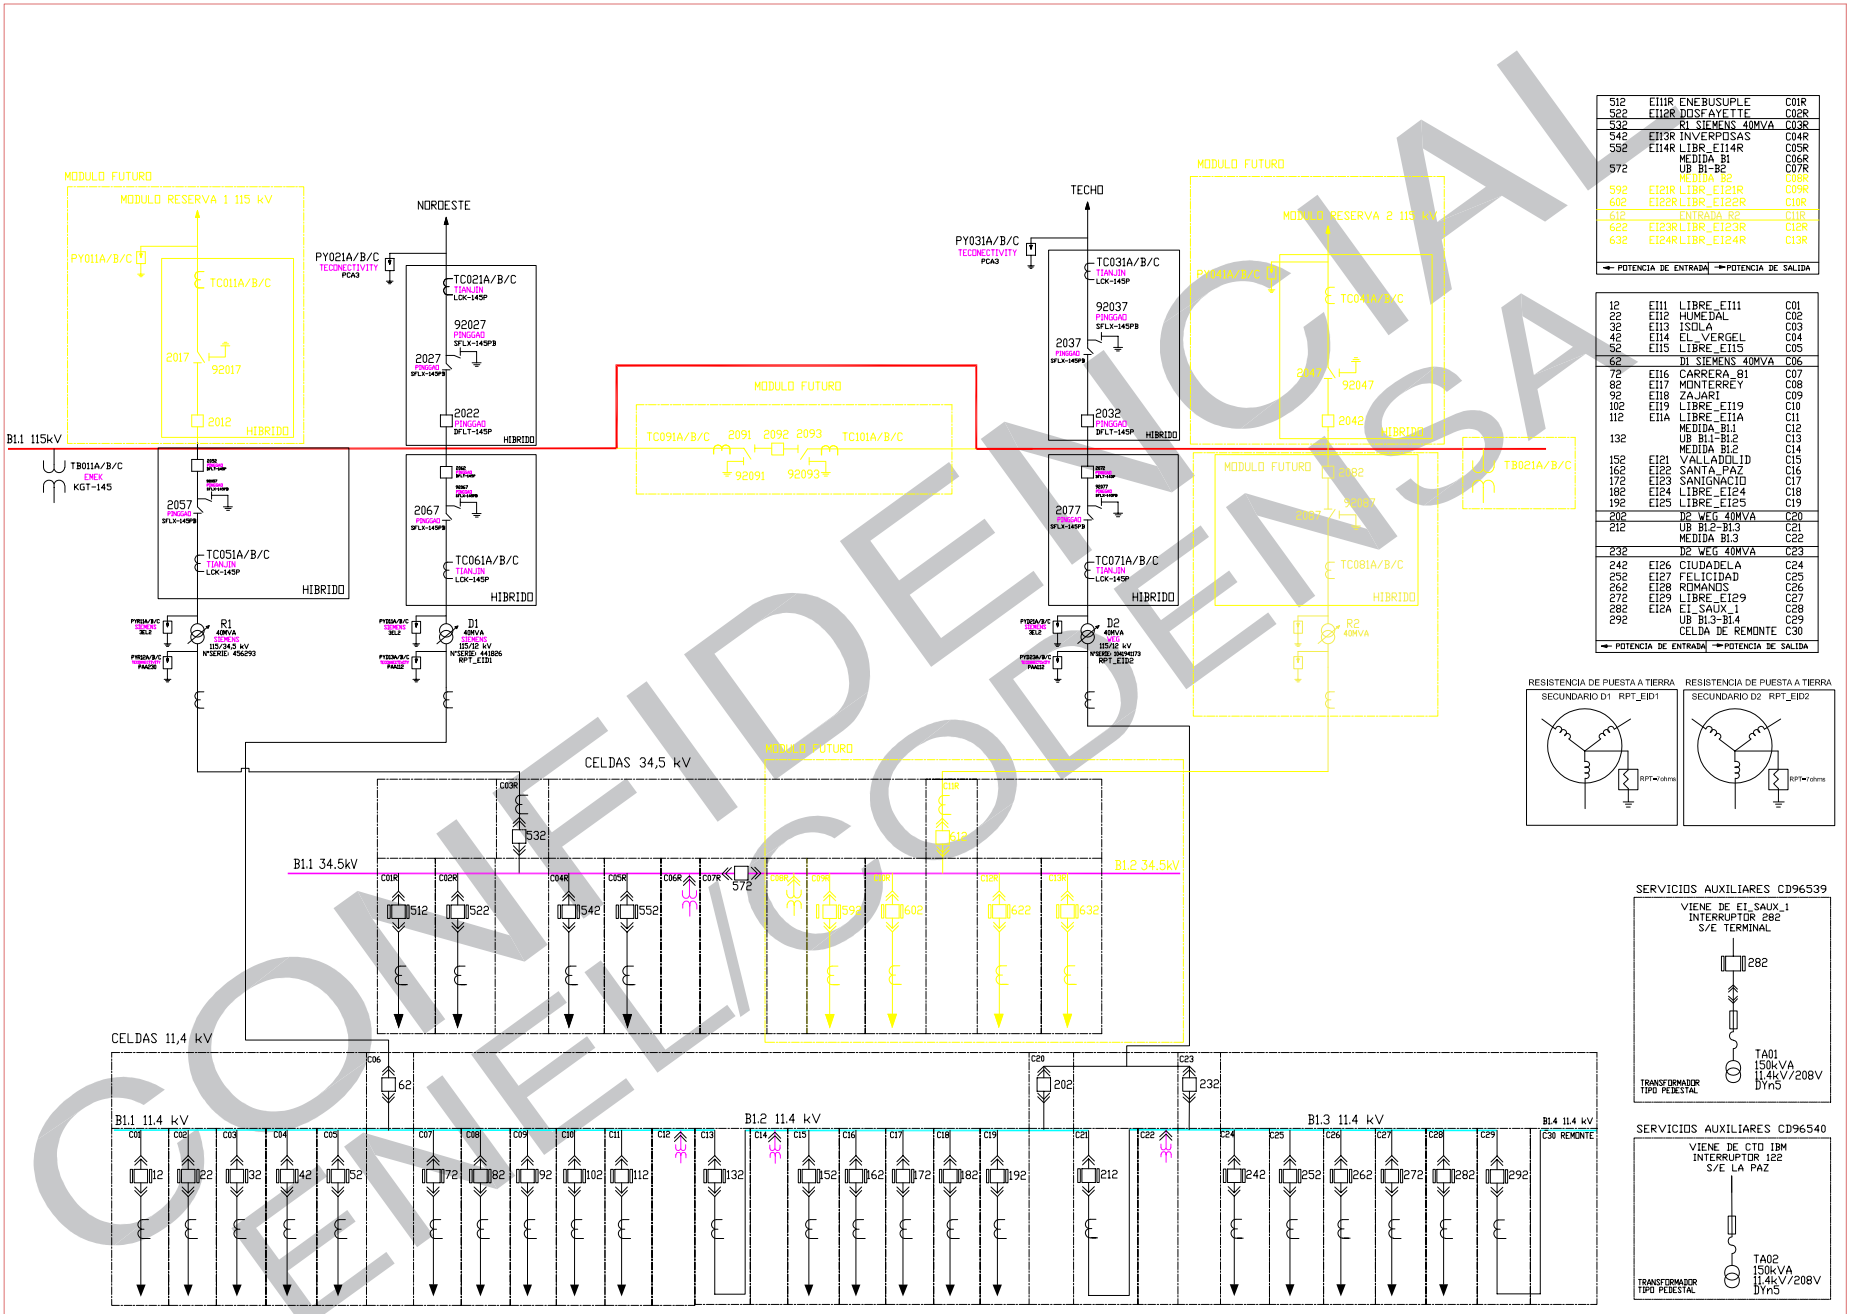

512	EI11R	ENEBUSUPLE	C01R
522	EI12R	DOSFAYETTE	C02R
532		R1 SIEMENS 40MVA	C03R
542	EI13R	INVERPOSAS	C04R
552	EI14R	LIBR_EI14R	C05R
		MEDIDA B1	C06R
572		UB B1-B2	C07R
		MEDIDA B2	C08R
592	EI21R	LIBR_EI21R	C09R
602	EI22R	LIBR_EI22R	C10R
612		ENTRADA R2	C11R
622	EI23R	LIBR_EI23R	C12R
632	EI24R	LIBR_EI24R	C13R

POTENCIA DE ENTRADA → POTENCIA DE SALIDA

12	EI11	LIBRE_EI11	C01
22	EI12	HUMEDAL	C02
32	EI13	ISOLA	C03
42	EI14	EL_VERGEL	C04
52	EI15	LIBRE_EI15	C05
62		D1 SIEMENS 40MVA	C06
72	EI16	CARRERA_81	C07
82	EI17	MONTERREY	C08
92	EI18	ZAJARI	C09
102	EI19	LIBRE_EI19	C10
112	EI1A	LIBRE_EI1A	C11
		MEDIDA B1.1	C12
132		UB B1.1-B1.2	C13
		MEDIDA B1.2	C14
152	EI21	VALLADOLID	C15
162	EI22	SANTA_PAZ	C16
172	EI23	SANIGNACIO	C17
182	EI24	LIBRE_EI24	C18
192	EI25	LIBRE_EI25	C19
202		D2 WEG 40MVA	C20
212		UB B1.2-B1.3	C21
		MEDIDA B1.3	C22
232		D2 WEG 40MVA	C23
242	EI26	CIUDADELA	C24
252	EI27	FELICIDAD	C25
262	EI28	ROMANOS	C26
272	EI29	LIBRE_EI29	C27
282	EI2A	EI_SAUX_1	C28
292		UB B1.3-B1.4	C29
		CELDA DE REMONTE	C30

POTENCIA DE ENTRADA → POTENCIA DE SALIDA

CONFIDENCIAL
ENEL/CODENSA

codensa

Unidad Organizativa
Administración Información
Técnica Col.

REVISION No. 5

FECHA: SEPTIEMBRE/2022

ARCHIVO: TERMINAL.DWG

\\COLCOD09FS01\FileServer\CONTROL UNIFILARES

DIAGRAMA UNIFILAR

SUBESTACION TERMINAL

Direccion: Av Calle 17 # 78G-33/45

TEL. PENDIENTE SIEMENS 6506

CODIGO: EI

141

HOJA: 1

DE: 1