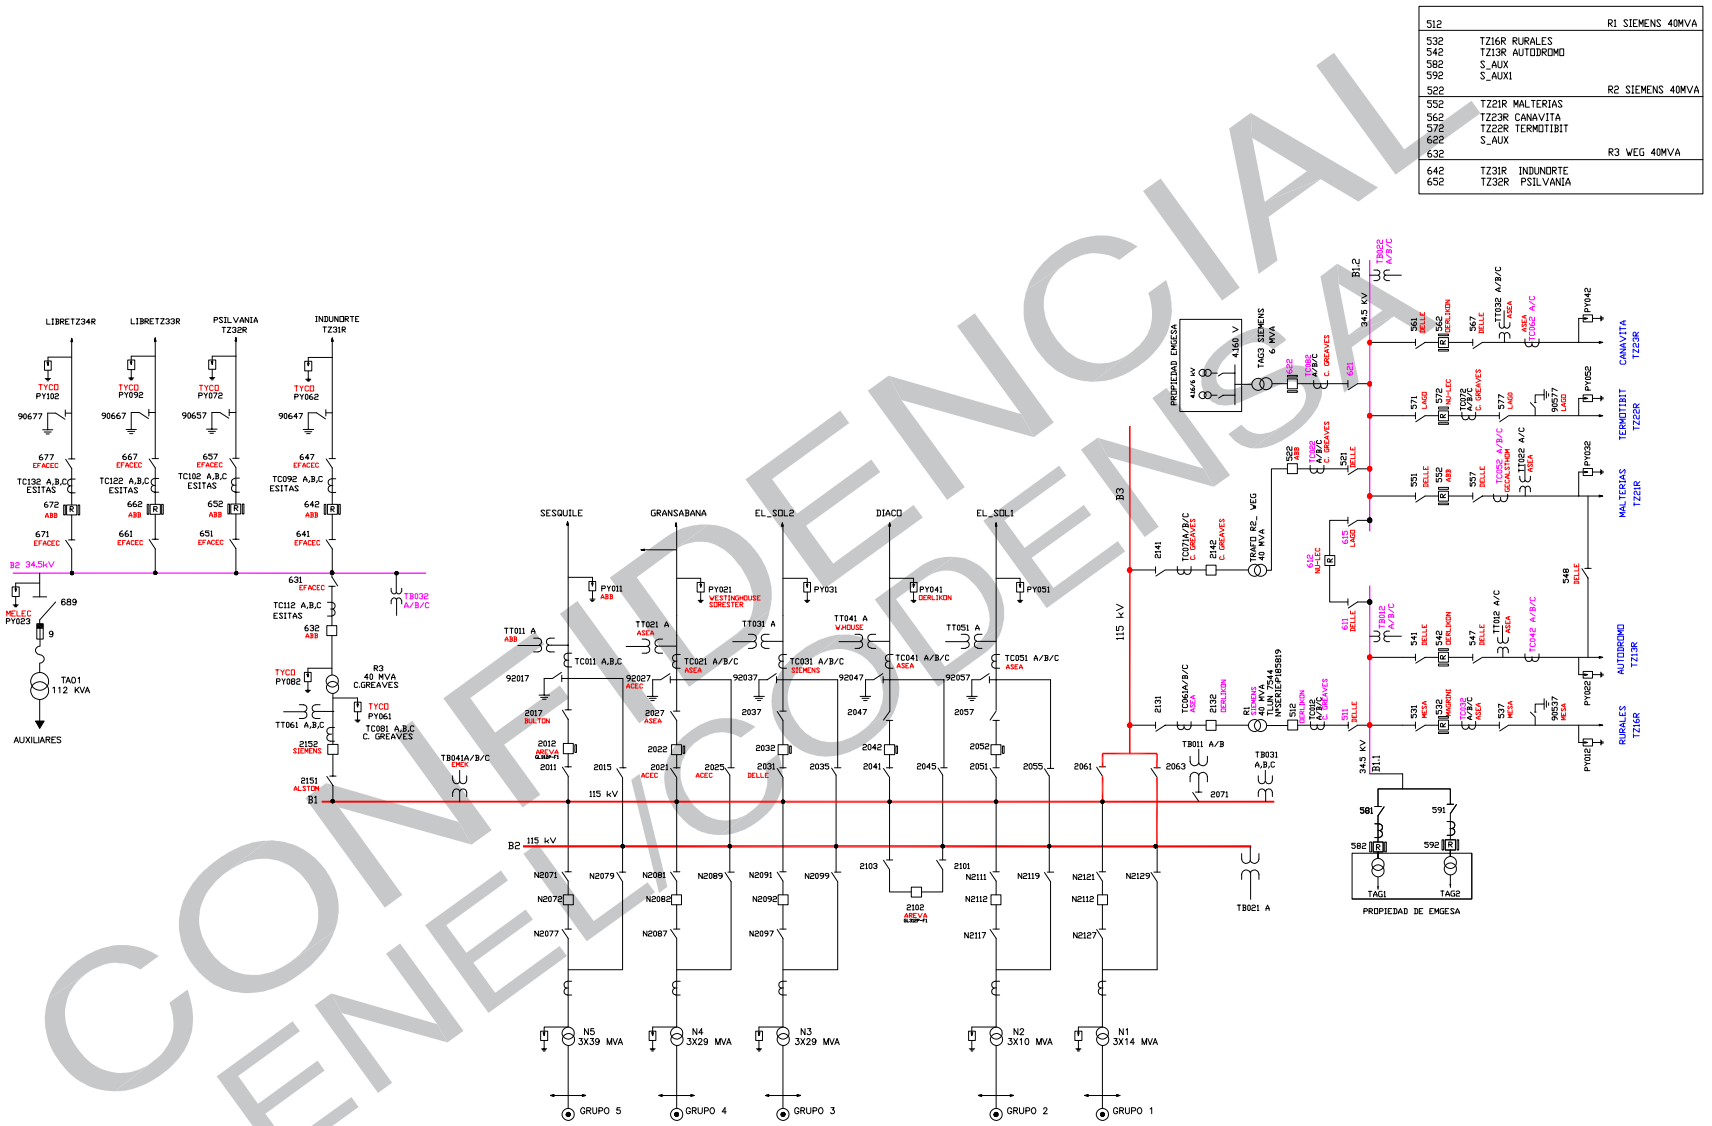

CONFIDENCIAL ENEL/CODENSA

enel codensa	Unidad Organizativa Administración Información Técnica Col.	REVISION No. 18
		FECHA: SEPTIEMBRE/2022
		ARCHIVO: TERMOZIPA.DWG
		\\COLCOD09FS01\FileServer\CONTROL UNIFILARES
		DIAGRAMA UNIFILAR
		SUBESTACION TERMOZIPA
		TEL: 6330736/34 SIEMENS 6584 CEL3158631279
		TOCANCIPA VDA VERGANZO KM 34
		CODIGO: TZ
		50
		HOJA: 1
		DE: 1