

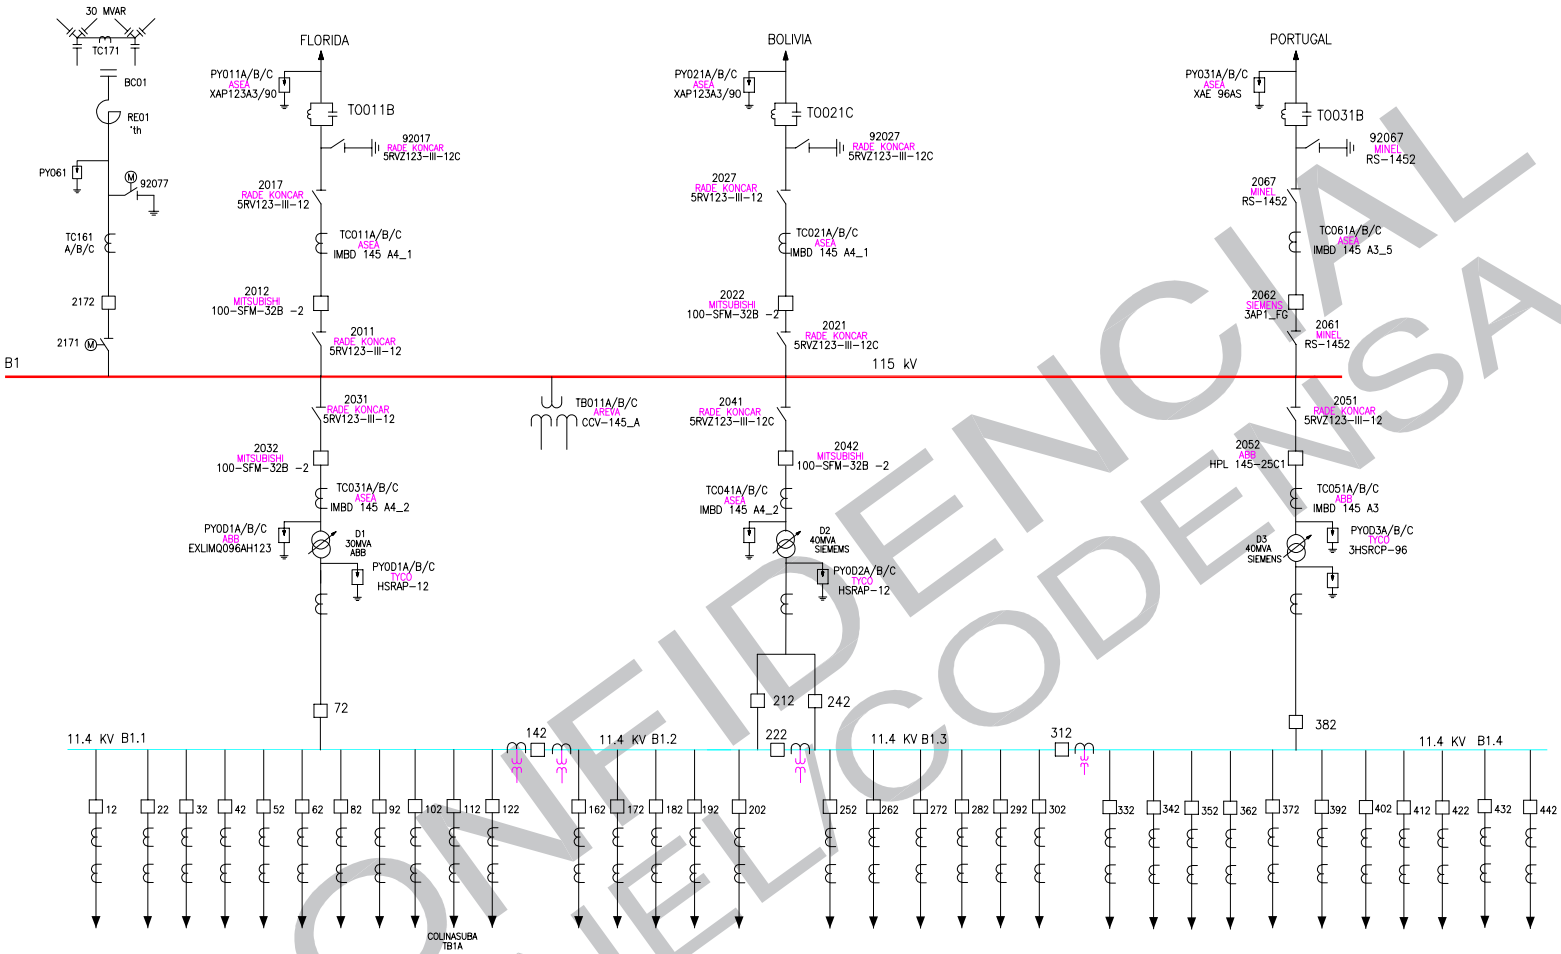


12	TB11 BC01_TB	C01
22	TB12 ALCAPARROS	C02
32	TB13 BERLIN	C03
42	TB14 PIEDRA_VER	C04
52	TB15 PORTAL	C05
62	TB16 UNIVERSAL	C06
72	ENTRADA D1 ABB 30MVA	C07
82	TB17 NUEVA_TIBA	C08
92	TB18 JAPON	C09
102	TB19 PLAZA_IMP	C10
112	TB1A COLINASUBA	C11
122	TB1B LIBRE_TB2	C12
	MEDIDA_B1.1	C13
142	UB B1.1-B1.2	C14
	MEDIDA_B1.2	C15
162	TB21 MANUELITA	C16
172	TB22 CTRO_SUBA	C17
182	TB23 BOCHALEMA	C18
192	TB24 LAS_FLORES	C19
202	TB25 TB_AUX_1	C20
212	ENTRADA D2 SIEMEMS 40 MVA	C21
222	UB B1.2-B1.3	C22
	MEDIDA_B1.3	C23
242	ENTRADA D2 SIEMEMS 40 MVA	C24
252	TB26 LA_GAITANA	C25
262	TB27 PUERTO _SOL	C26
272	TB28 J_AMARILLO	C27
282	TB29 ALMENDROS	C28
292	TB2A BUSES_SUBA	C29
302	TB2B BC02_TB	C30
312	UB B1.3-B1.4	C31
	MEDIDA_B1.4	C32
332	TB31 RUBI_NORTE	C33
342	TB32 STA_INES	C34
352	TB33 VL_MARIA	C35
362	TB34 TB_AUX_2	C36
372	TB35 COSTA_AZUL	C37
382	ENTRADA D3	C38
392	TB36 RINCON	C39
402	TB37 LINDARAJA	C40
412	TB38 URB_LAROSA	C41
422	TB39 BQUE_SUBA	C42
432	TB3A HAMMEN	C43
442	TB3B BC03_TB	C44


CD: 320

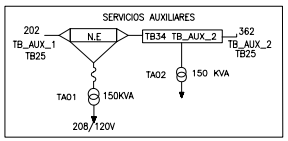


TRASFORMADOR DESENERGIZADO

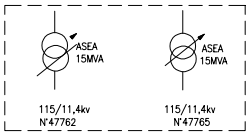

RESISTENCIAS PUESTA A TIERRA

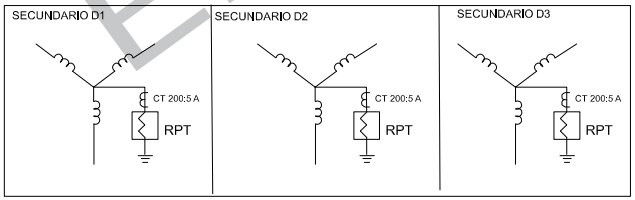

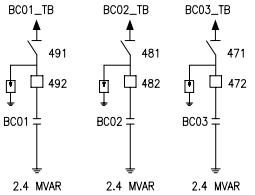

NOTA: NO REPRESENTAR EN GESQ

BT01	BANCO DE BATERIAS
BT02	BANCO DE BATERIAS
TA01	TRANSFORMADOR DE SERVICIOS AUXILIARES
SA01	CELDA DE SERVICIOS AUXILIARES Vac
SC01	CELDA DE SERVICIOS AUXILIARES Vdc
RVD1	CELDA DE CAMBIADOR DE TOMAS TRAFO D1
RVD2	CELDA DE CAMBIADOR DE TOMAS TRAFO D2
CB01	CARGADOR DE BATERIAS

CONFIDENCIAL
ENEL CODENSA

codensa
Grupo Enel

Unidad Organizativa
Administración Información
Técnica Col.

REVISION No. 22
FECHA: NOVIEMBRE/2022
ARCHIVO: TIBABUYES.DWG
\\COLCOD09FS01\FileServer\CONTROL UNIFILARES

DIAGRAMA UNIFILAR
SUBESTACION TIBABUYES
CARRERA 108 CALLE 122
TEL. 6899793 SIEMENS 6586
CODIGO: TB

51
HOJA: 1
DE: 1