


19	AUXILIARES
22	TMID 3. ESQUINAS
32	TMED2 S. JERONIMO (ANTIGUO IDECAMA URBANO)
41	DI SIEMENS 3/5MVA 34.5/138kV
51	UB-BI.1, BI.2
61	D2 TTY 3MVA 34.5/138kV
72	TMED2 CACHIBULO (ANTIGUO TALDEQUEMAD)
82	TMED2 VASQUEZ (ANTIGUO SAN FERNANDO)

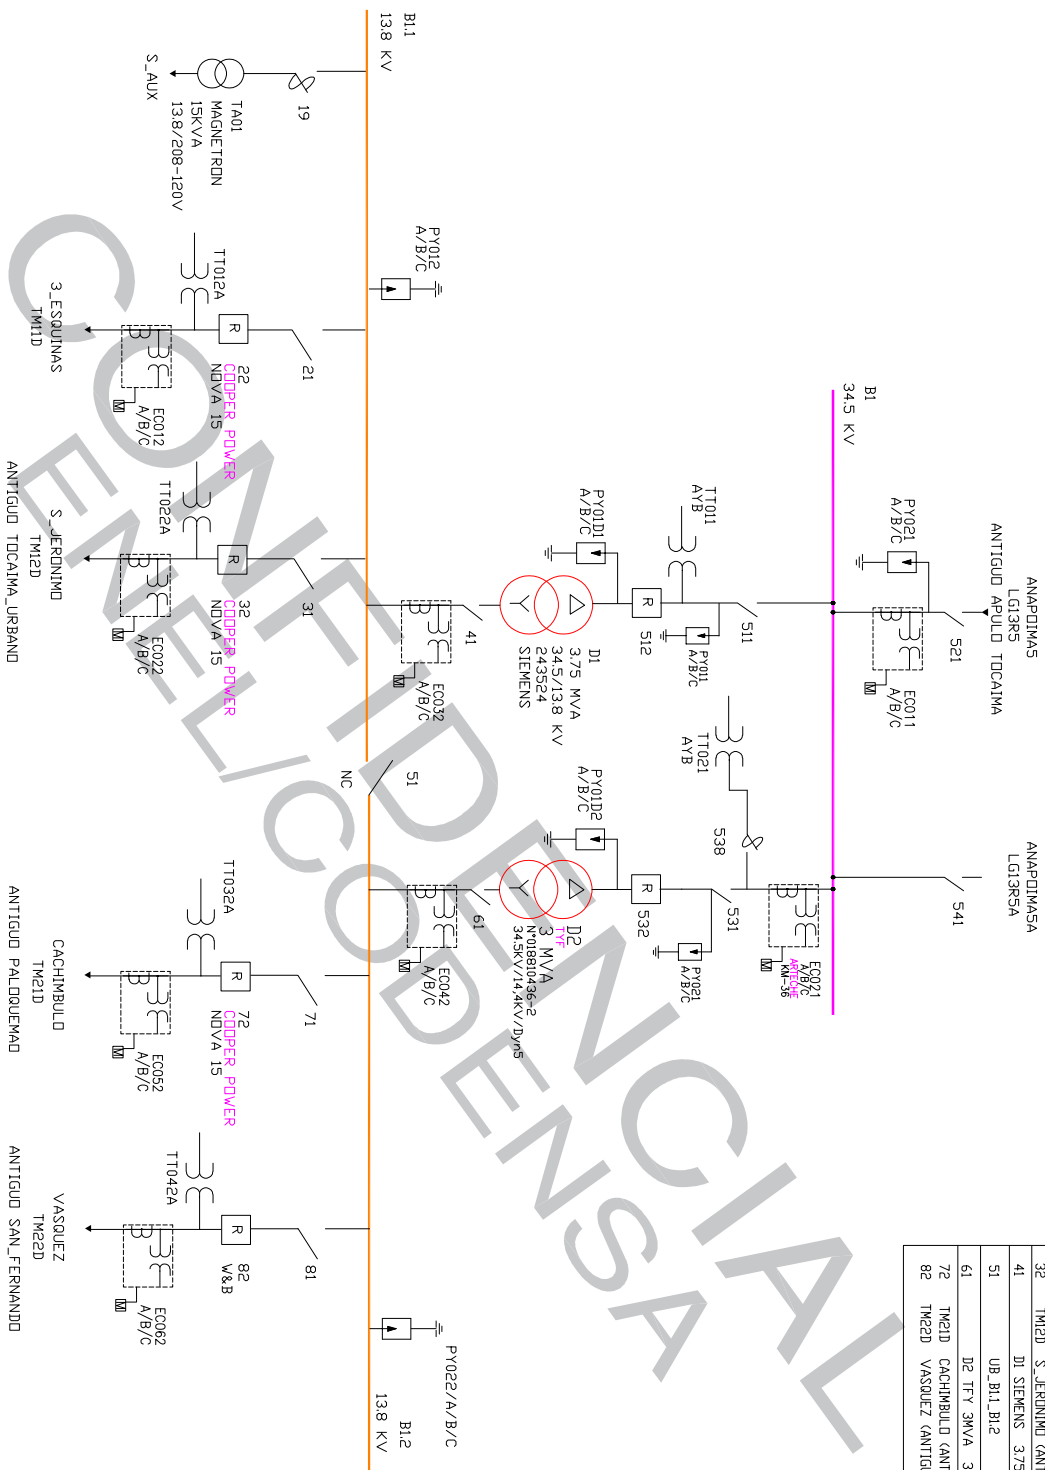

Unidad Organizativa
Administracion Informacion
Tecnica Col

REVISION No. 8

FECHA: ENERO/2022

ARCHIVO:
TOCAIMA.DWG

DIAGRAMA UNIFILAR

SUBESTACION TOCAIMA

MUNICIPIO DE TOCAIMA

CODIGO: **TM**

632

HOJA: 1

De: