
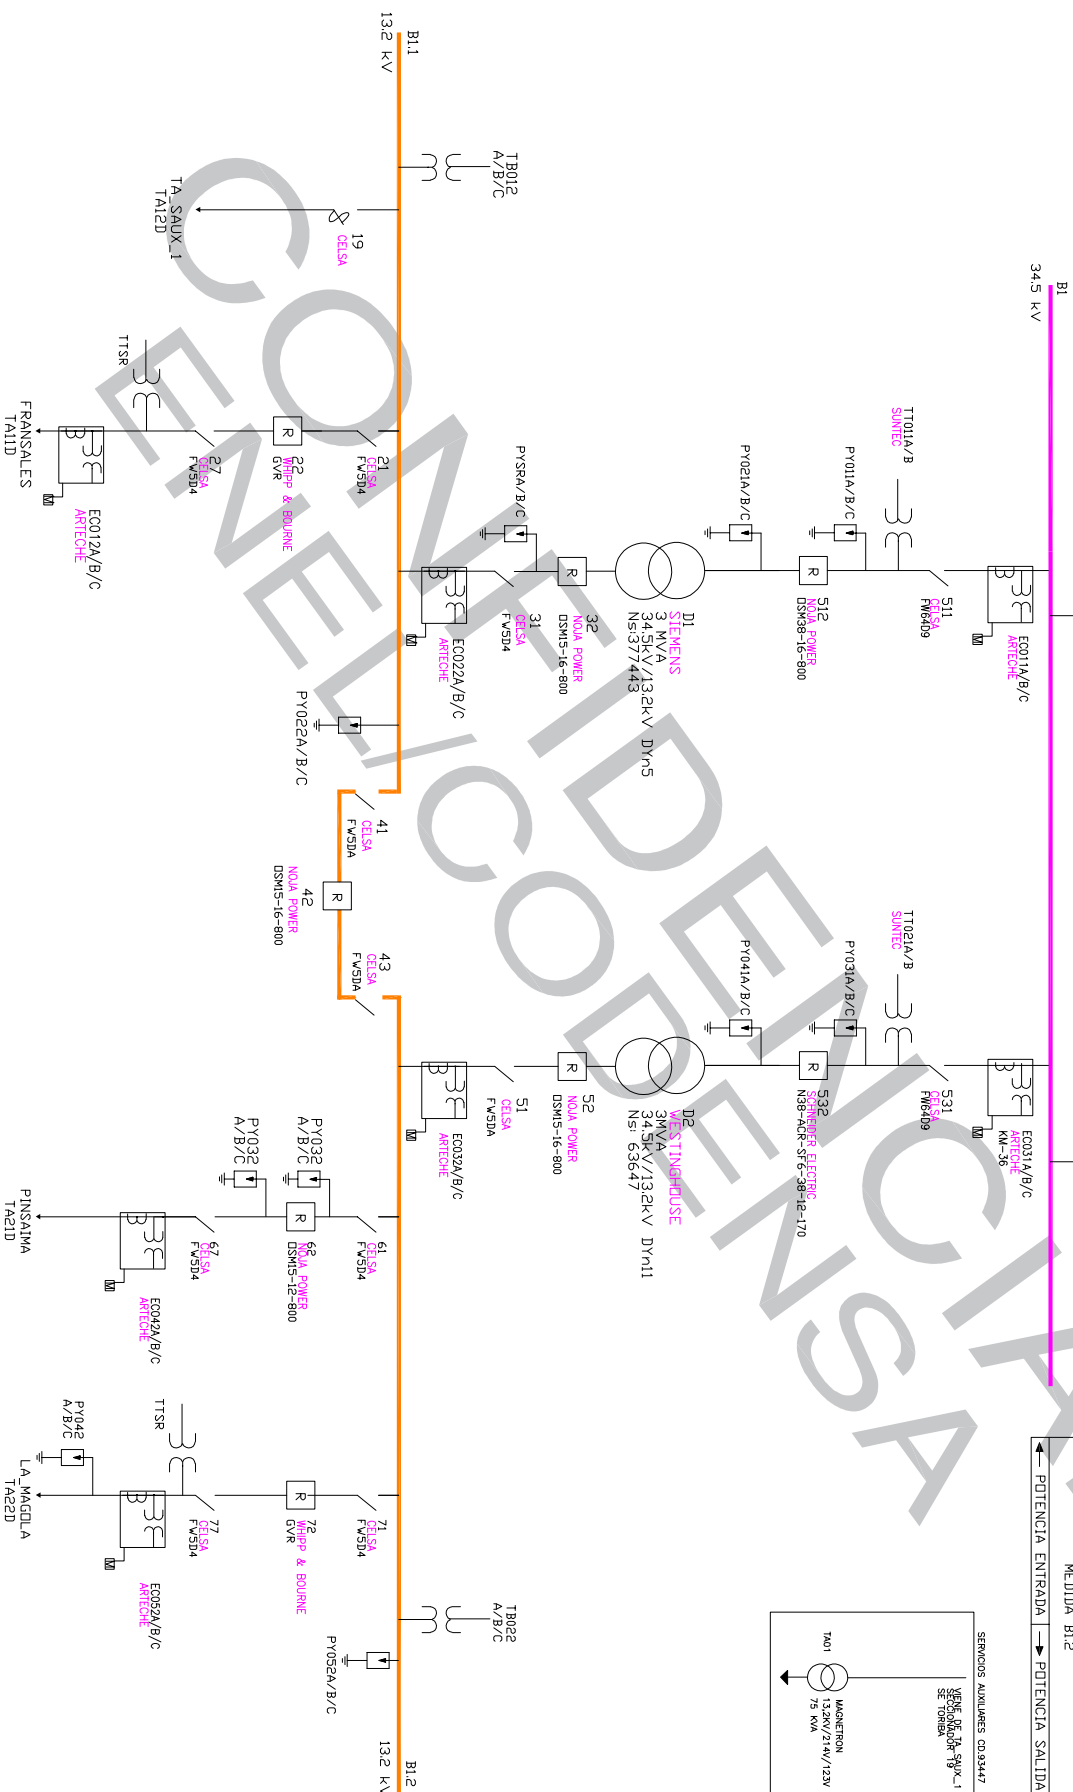


512	D1 SIEMENS 3MVA	→
522	TJUE4 BIMBO 4	→
532	D2 WESTINGHOUSE 3MVA	→
542	TA0R LIBRE.T01	→
19	TA_S AUX_1	→
22	FRANSALES	→
32	D1 SIEMENS 3MVA	→
42	UB B11-B12	→
52	D2 WESTINGHOUSE 3MVA	→
62	TA2D PINSAIMA	→
72	LA MAGOLA	→
72	TA22D	→
MEIDA B12		→
← POTENCIA ENTRADA		POTENCIA SALIDA

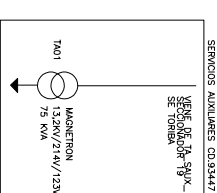

Unidad Organizativa
Administración Informática
Técnica Col

REVISION No.	10	DIAGRAMA UNIFILAR	619
FECHA:	NOVIEMBRE/2022	SUBESTACION TORIBA ANTIGUO SFRANCISEEC	HOLA: 1
ARCHIVO:	TORIBA.DWG	MUNICIPIO DE SAN FRANCISCO	DE: 1
C:\ESQUEMAS SUBESTACIONES\ESQUEMAS DEFINITIVOS			
CODIGO:	TA		