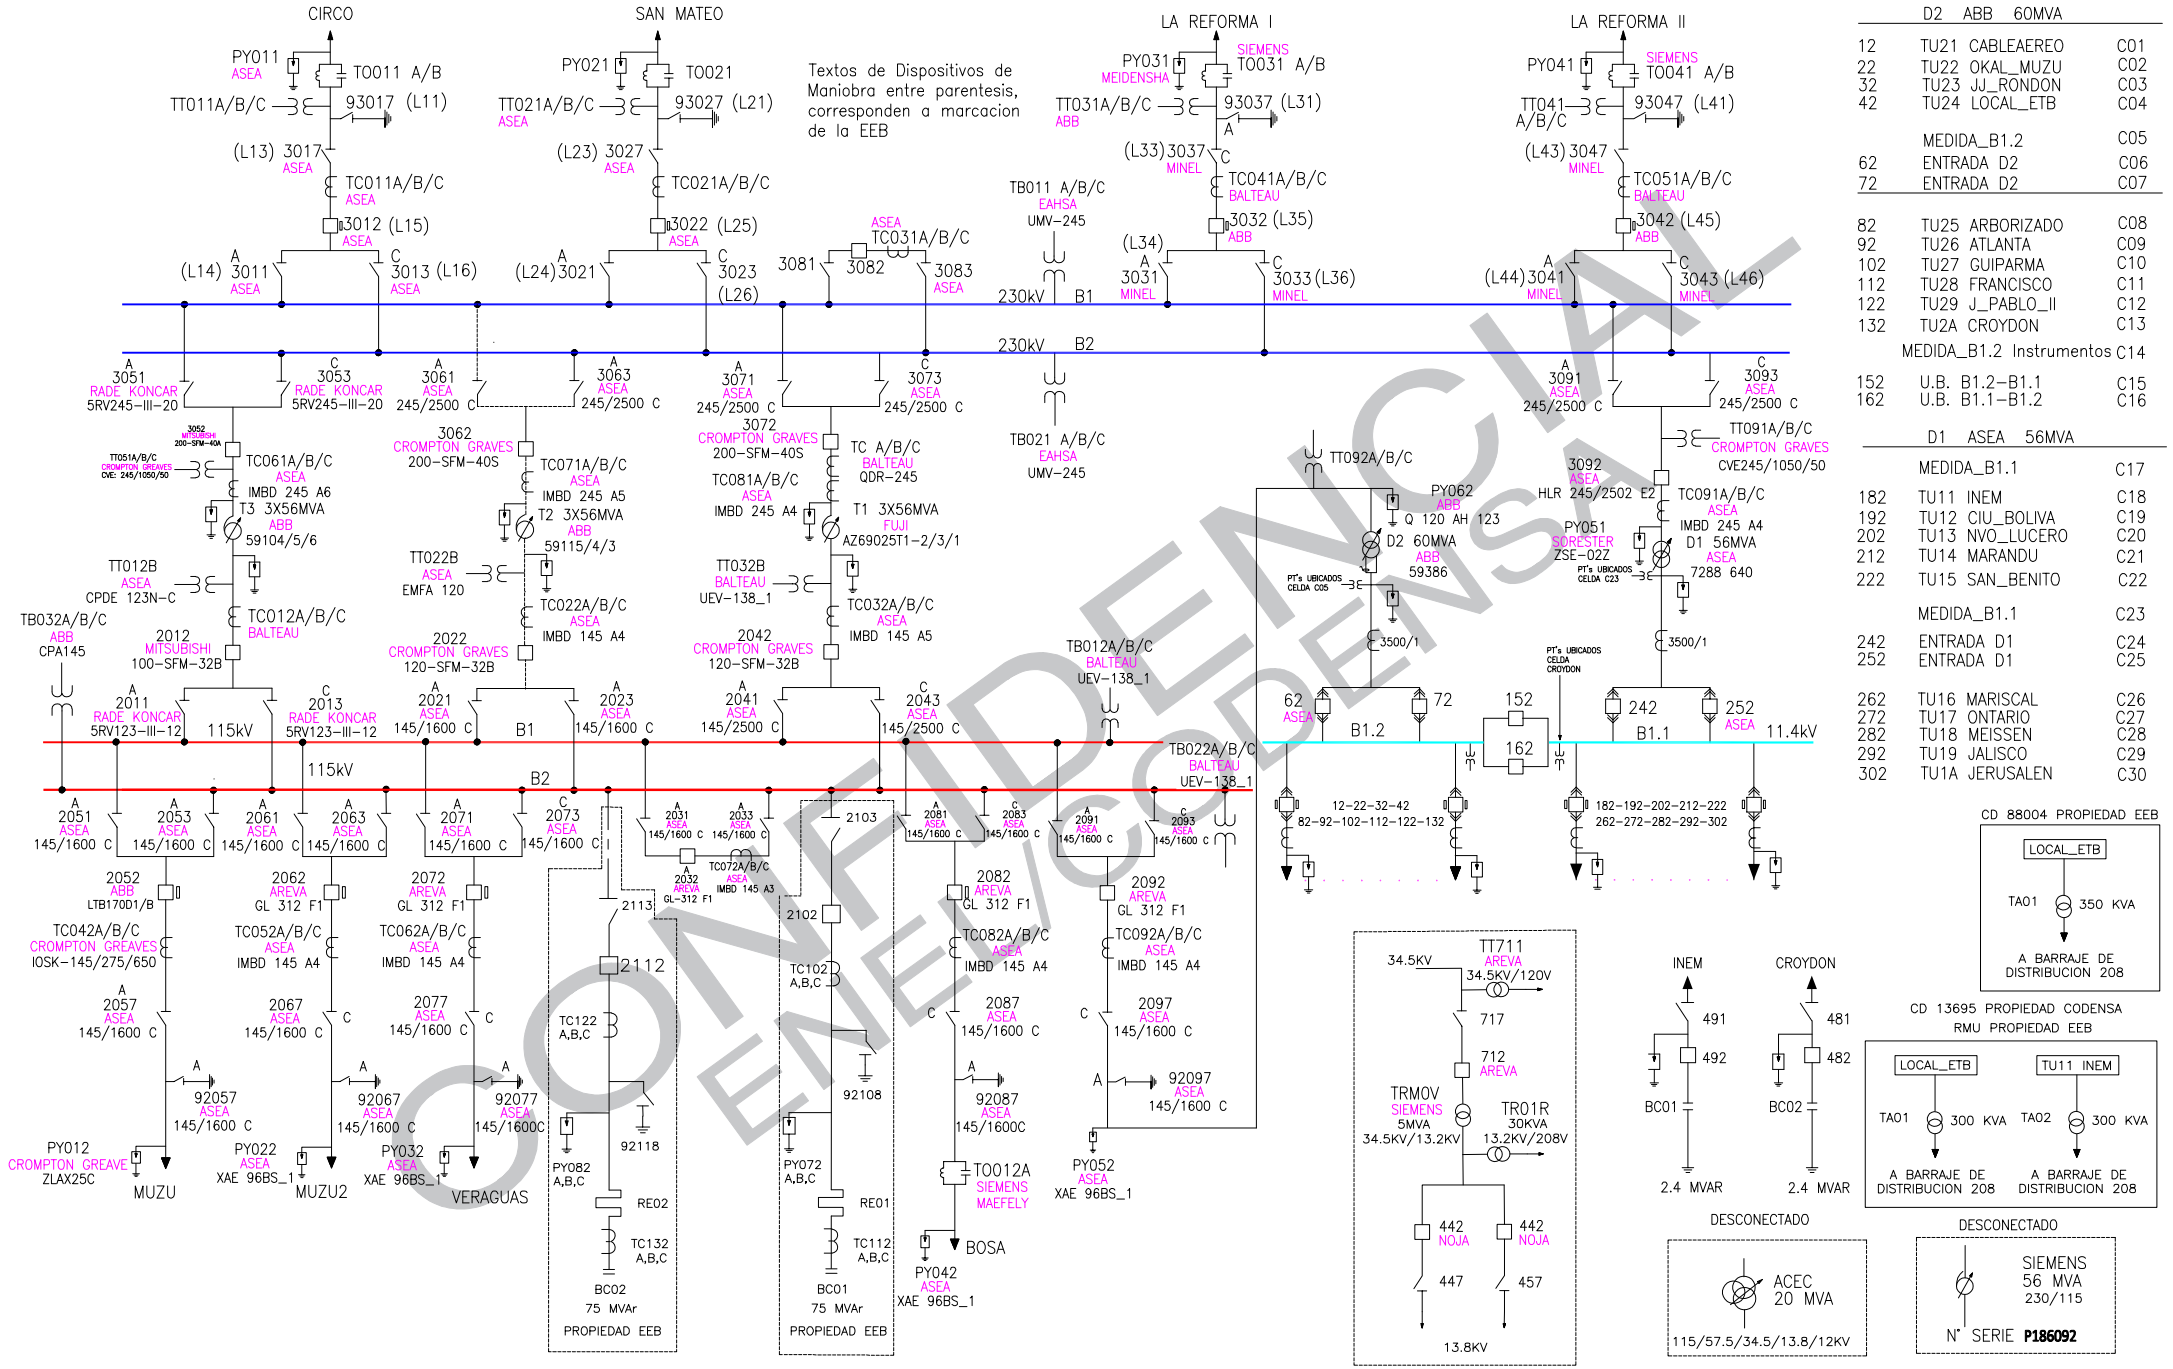

D2 ABB 60MVA		
12	TU21 CABLEAEREO	C01
22	TU22 OKAL_MUZU	C02
32	TU23 JJ_RONDON	C03
42	TU24 LOCAL_ETB	C04
	MEDIDA_B1.2	C05
62	ENTRADA D2	C06
72	ENTRADA D2	C07
82	TU25 ARBORIZADO	C08
92	TU26 ATLANTA	C09
102	TU27 GUIPARMA	C10
112	TU28 FRANCISCO	C11
122	TU29 J_PABLO_II	C12
132	TU2A CROYDON	C13
	MEDIDA_B1.2 Instrumentos	C14
152	U.B. B1.2-B1.1	C15
162	U.B. B1.1-B1.2	C16

D1 ASEA 56MVA		
	MEDIDA_B1.1	C17
182	TU11 INEM	C18
192	TU12 CIU_BOLIVA	C19
202	TU13 NVO_LUCERO	C20
212	TU14 MARANDU	C21
222	TU15 SAN_BENITO	C22
	MEDIDA_B1.1	C23
242	ENTRADA D1	C24
252	ENTRADA D1	C25
262	TU16 MARISCAL	C26
272	TU17 ONTARIO	C27
282	TU18 MEISSEN	C28
292	TU19 JALISCO	C29
302	TU1A JERUSALEN	C30

CONFIDENCIAL ENEL CODENSA

codensa

Unidad Organizativa Administración Información Técnica Col.

REVISION No. 27

FECHA: OCTUBRE/2022

ARCHIVO: TUNAL.DWG

\\COLCODO9FS01\FileServer\CONTROL UNIFILARES

DIAGRAMA UNIFILAR

SUBESTACION TUNAL

AV BOYACA P/QUE TUNAL CII 55 S #20-51

TEL. 7602722/7677563 SIEMENS 6590

CODIGO: TU

53

HOJA: 1

DE: 1