512		R1 SIEMENS 40MVA	
522	UB11R	TAUSA	
		MEDIDA B1.1	
532	UB12R	CAPELLANIA	
572		UB B1.1–B1.2	
542	UB21R	ORIENTE	
552		R2 SIEMENS 30MVA	
562	UB22R	SIATAMA	
579	UB23R	UB_SAUX_1	
		MEDIDA B1.2	
82	UB11D	UBATE_LCAL	C01
92	UB12D	CARUPA	C02
102	UB13D	CUCUNUBA	C03
112		D1 SIEMENS 12MVA	C04
		MEDIDA_B1.1	C05
132	UB14D	LENGUAZAQ	C06
142	UB15D	SUTATAUSA	C07
152	UB16D	FUQUENE	C08

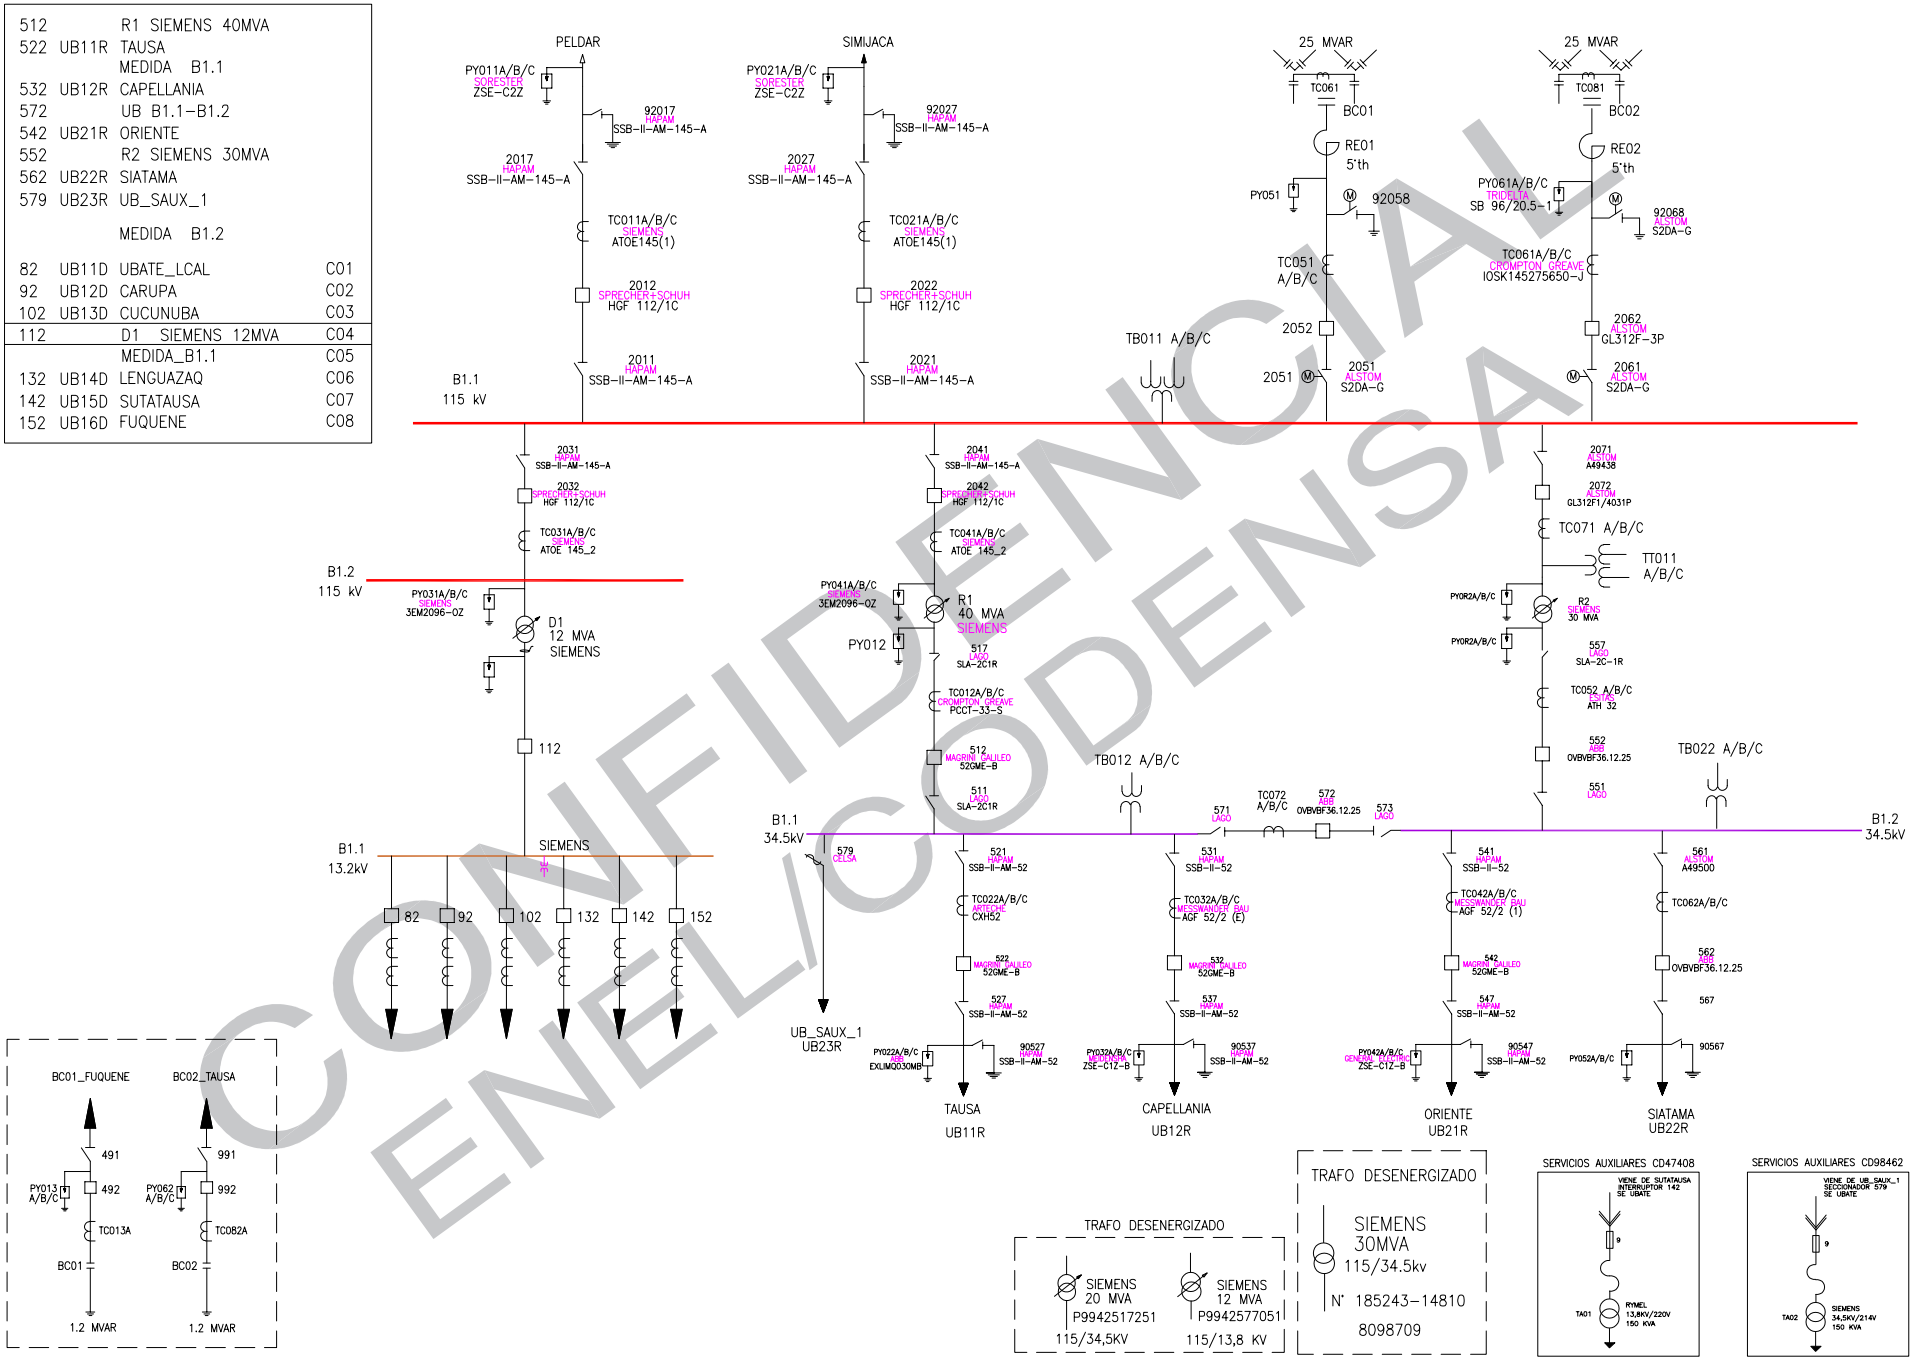

CONFIDENCIAL
ENEL/CODENSA

codensa

Unidad Organizativa
Administraciòn Informaciòn
Tècnica Col

REVISION No.	27
FECHA:	DICIEMBRE/2022
ARCHIVO:	UBATE.DWG
	F:\\FileServer\CONTROL UNIFILARES\UNIFILARES_MARZO_2019

DIAGRAMA UNIFILAR
SUBESTACION UBATE
MUNICIPIO DE UBATE
SIEMENS 6609

CODIGO: UB

55

HOJA: 1

DE: 1