


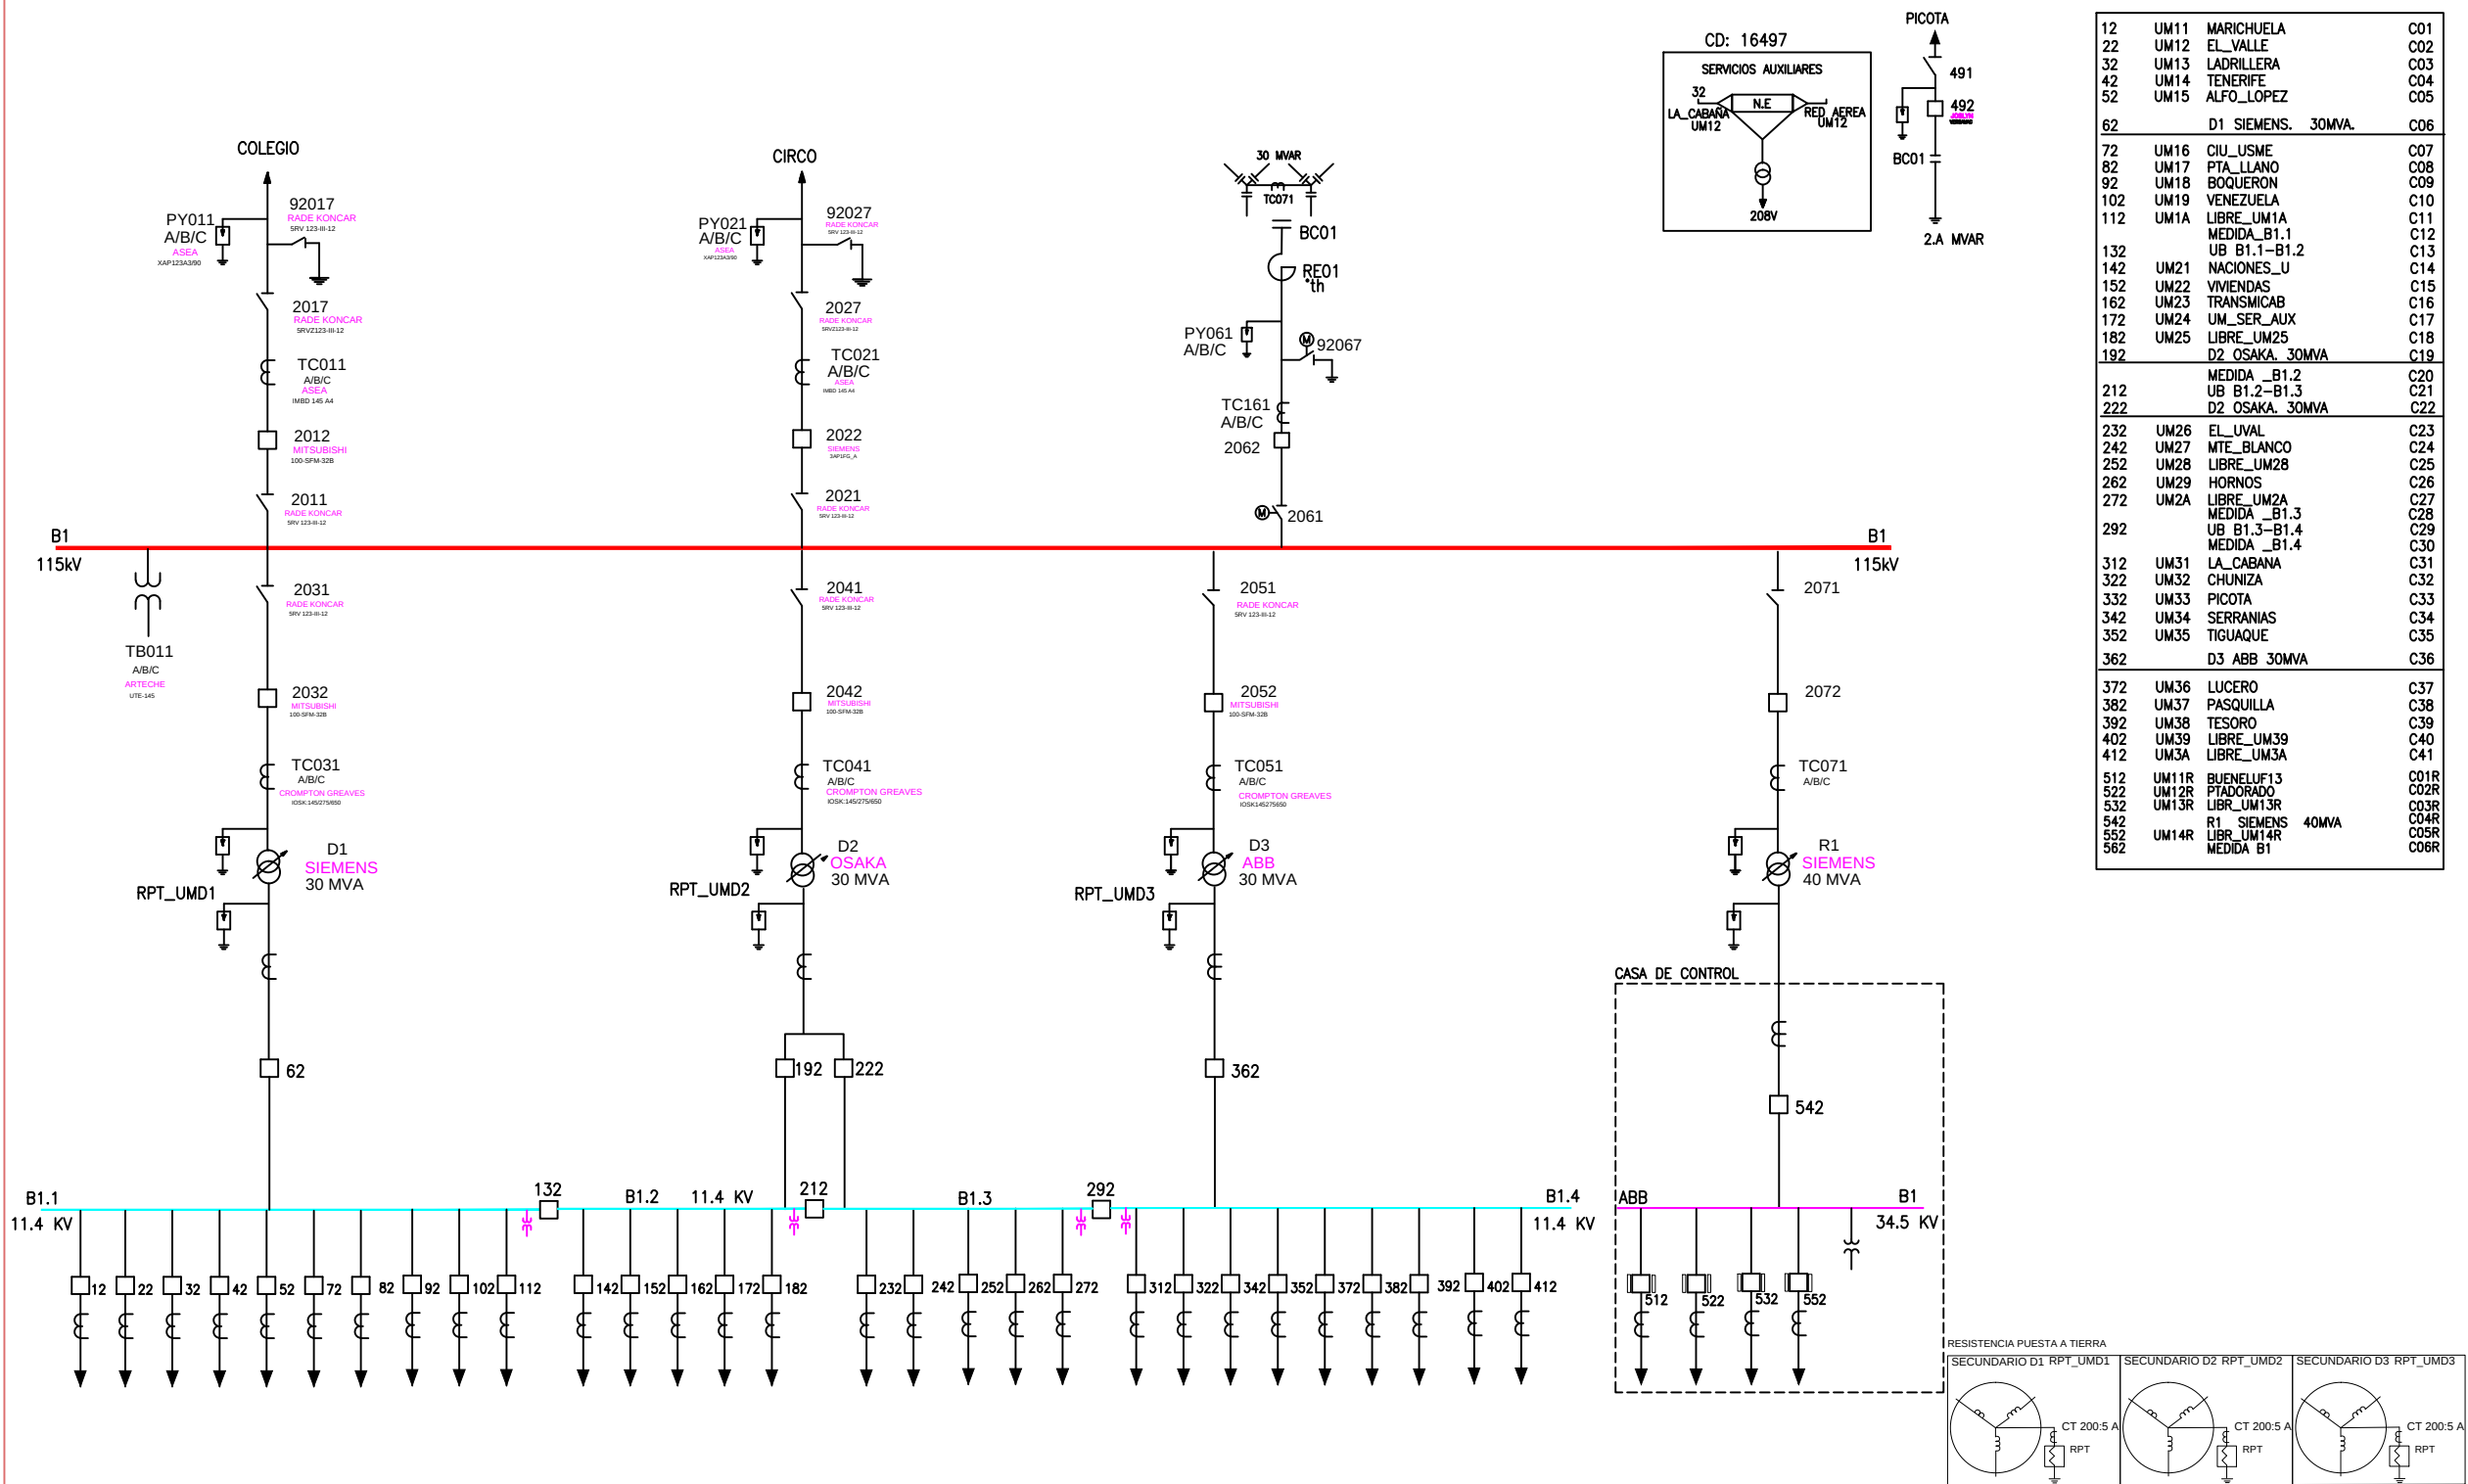

Unidad Organizativa
Administración Información
Técnica Col.

REVISION No. 23
FECHA: JUNIO/2021
ARCHIVO: USME.DWG
Y:\\FileServer\\CONTROL UNIFILARES\\UNIFILARES_DICIEMBRE_2019

DIAGRAMA UNIFILAR
SUBESTACION USME
CARRERA 27C ESTE No. 91L-35 SUR
TEL. 2004010 SIEMENS 6594
CODIGO: UM

57

HOJA: 1
DE: 1