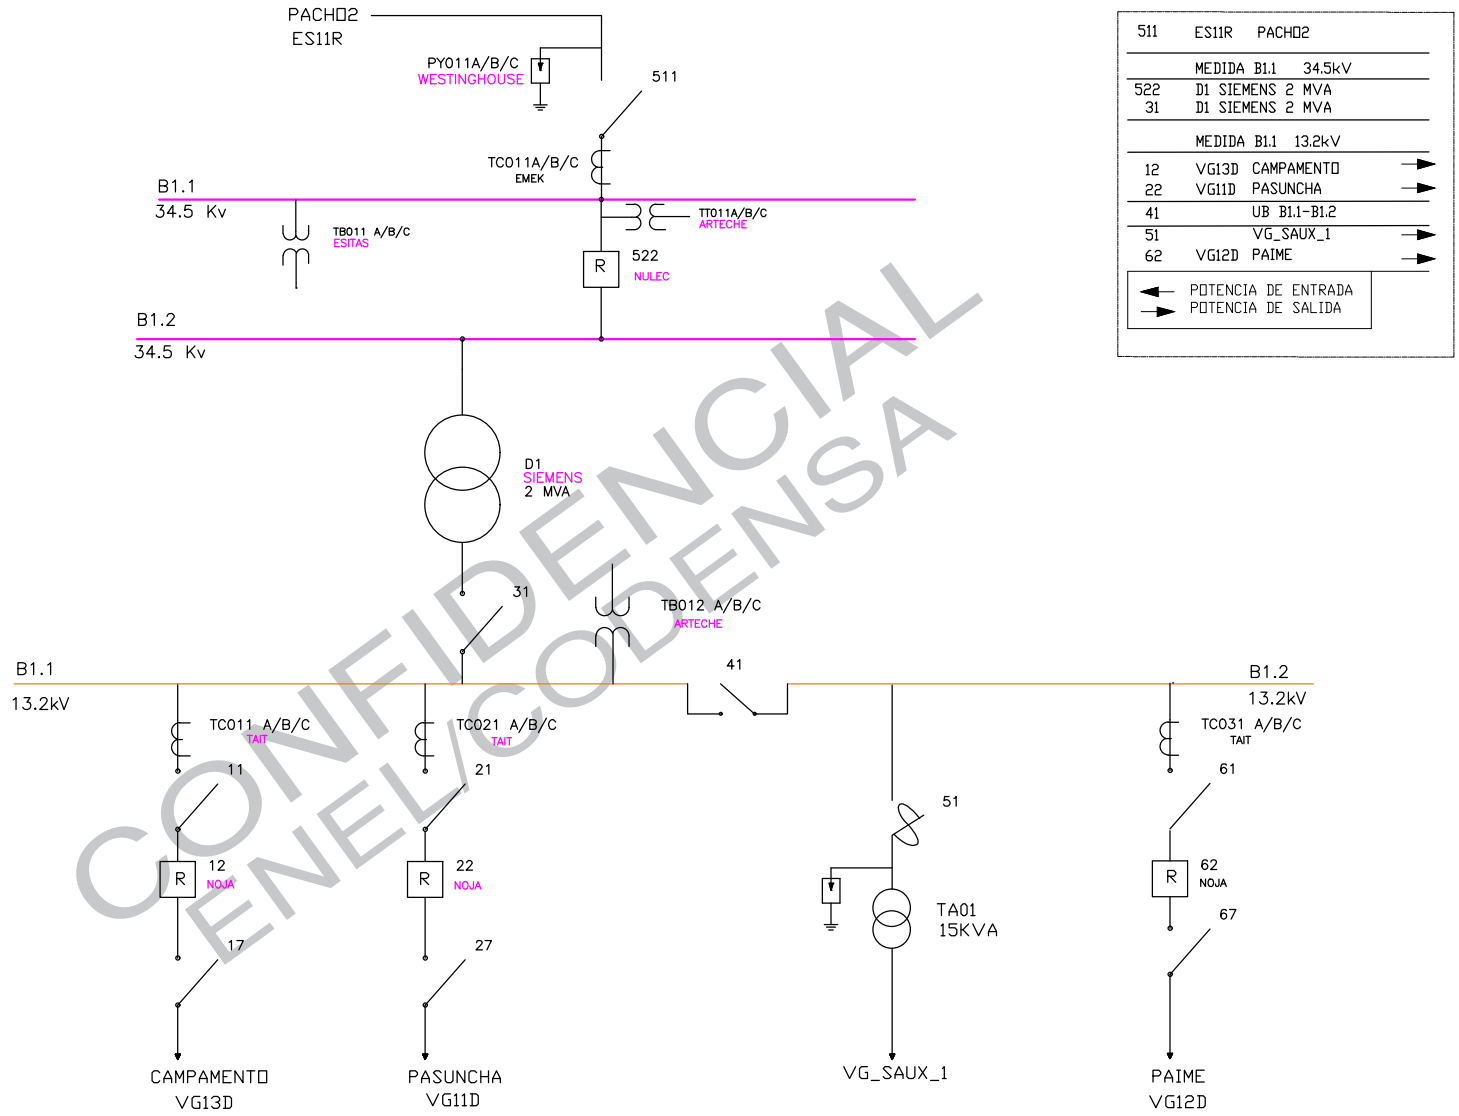


CONFIDENCIAL
ENEL/CODENSA

enel codensa	Unidad Organizativa Administración Información Técnica Col.	REVISION No. 11	DIAGRAMA UNIFILAR	114
		FECHA: MAYO/2019	SUBESTACION VILLAGOMEZ	
		ARCHIVO: VILLAGOMEZ.DWG C:\ESQUEMAS SUBESTACIONES\CONTROL UNIFILARES	M/CIPIO VILLAGOMEZ LADO CTR. DE SALUD	HOJA: 1
			CODIGO: VG	DE: 1