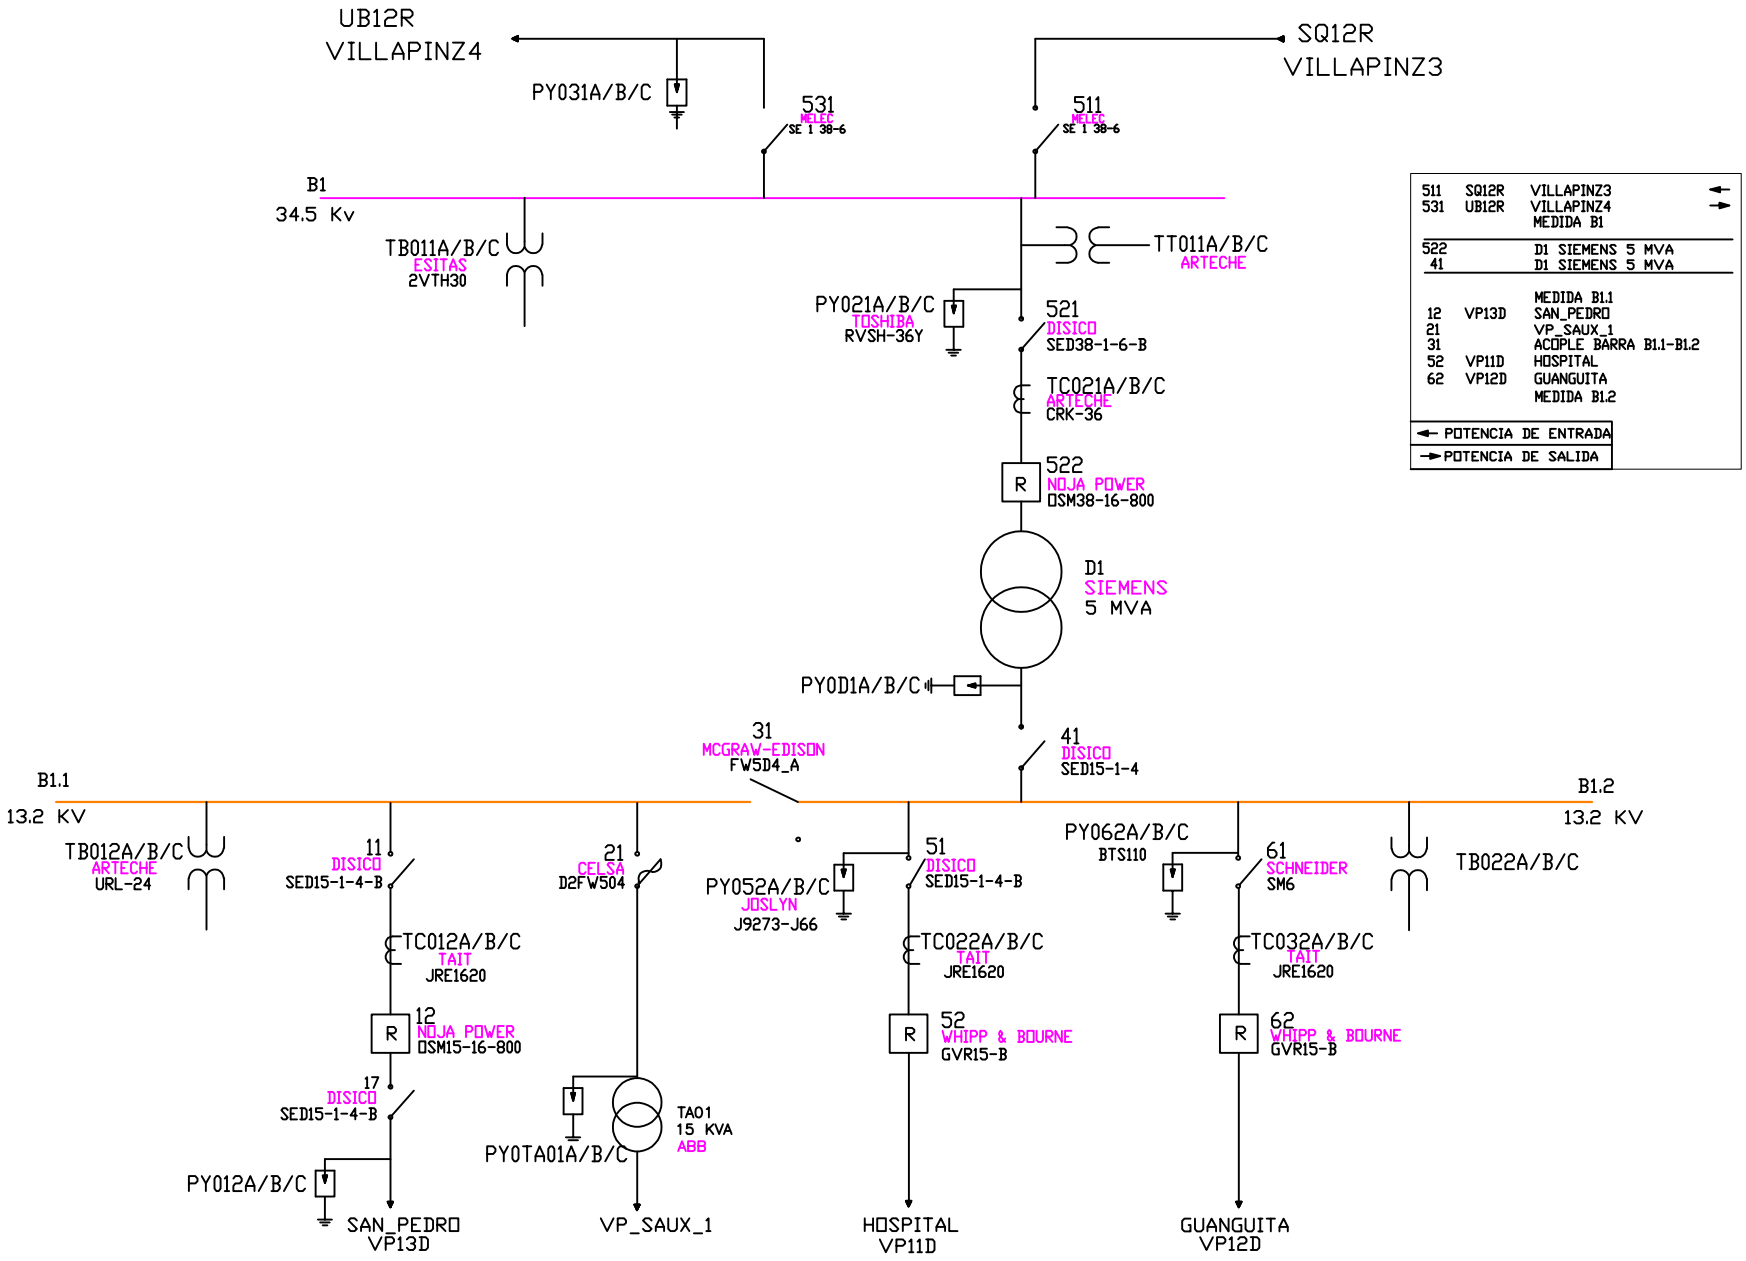


enel codensa	Unidad Organizativa Administración Información Técnica Col.	REVISION No. 13	DIAGRAMA UNIFILAR
		FECHA: ENERO/2022	SUBESTACION VILLAPINZON
		ARCHIVO: VILLAPINZON.DWG	C.M/PAL VILLAPINZON FRENTE A PLAZA DE MERCADO
		C:\ESQUEMAS SUBESTACIONES\ESQUEMAS DEFINITIVOS	CODIGO: VP
			115
			HOJA: 1
			DE: 1