



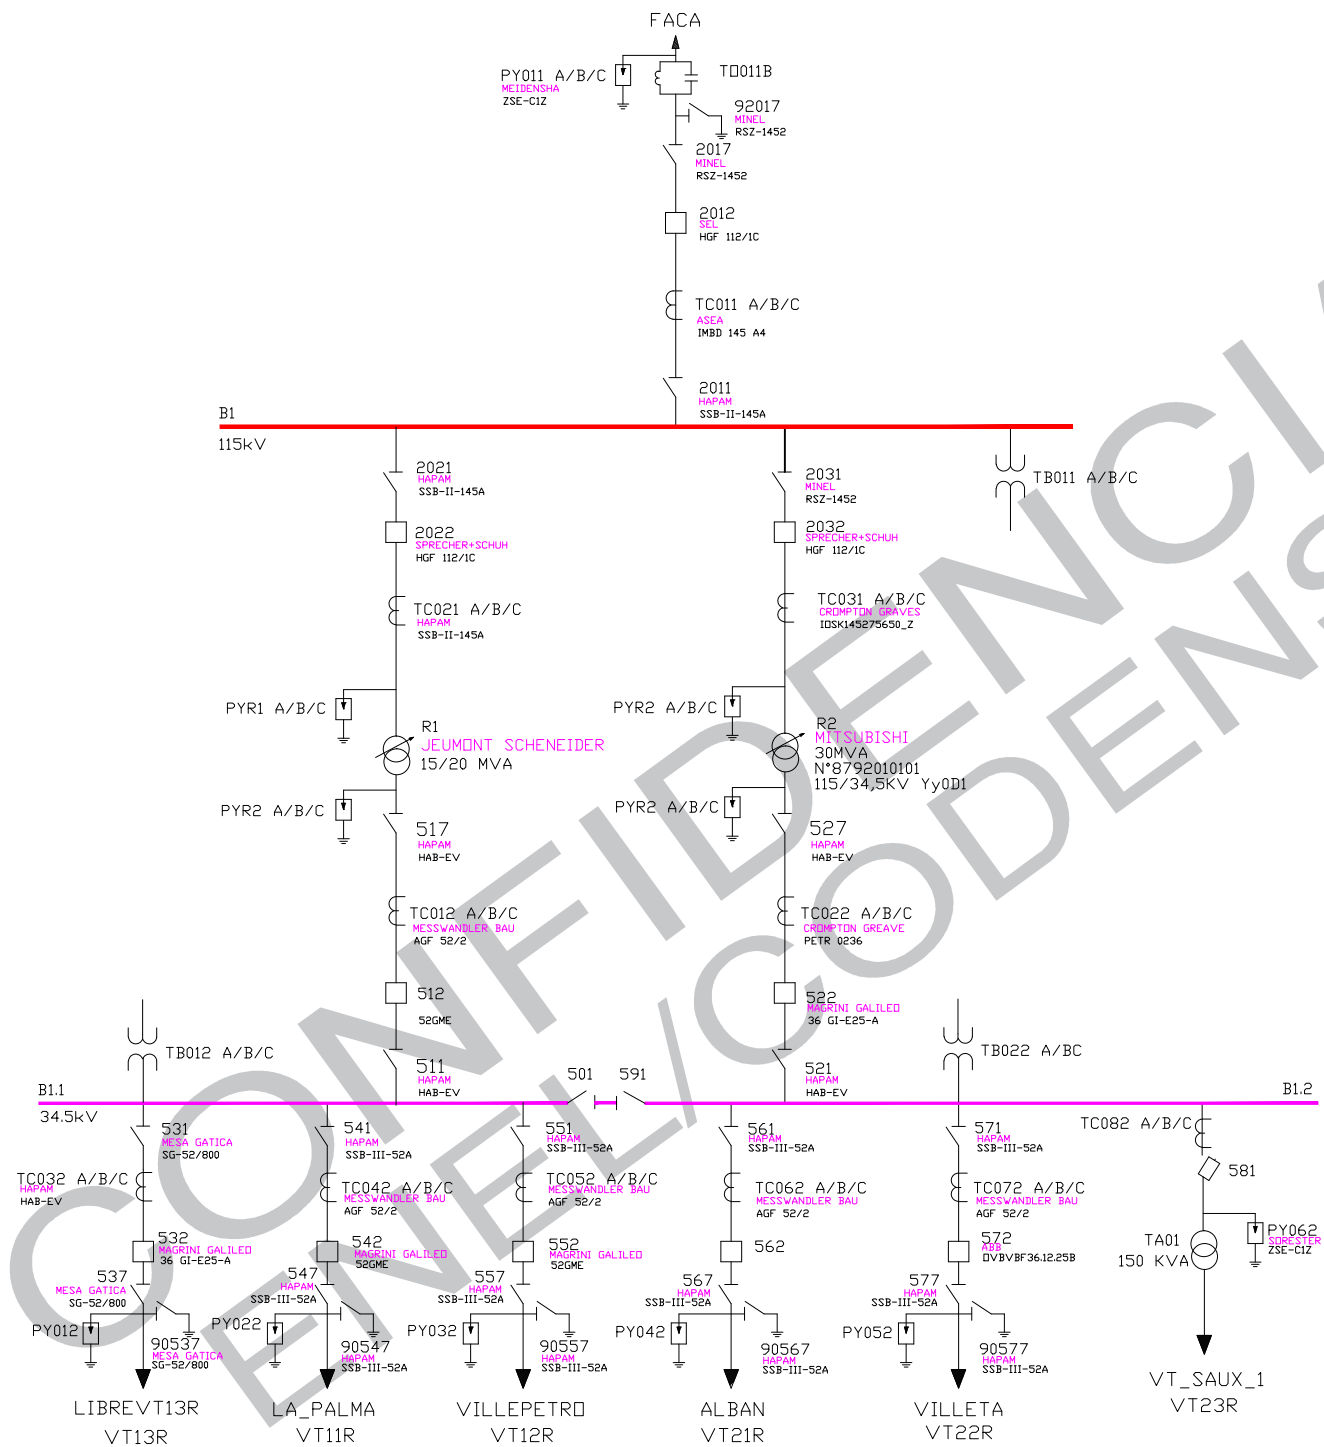

542	VT11R	LA_PALMA	→
552	VT12R	VILLAPETRO	→
532	VT13R	LIBRETV13R	→
MEDIDA B1.2			
562	VT21R	ALBAN	→
572	VT22R	VILLETA	→
581	VT23R	VT_SAUX_1	→
591	UB-B1.1-B1.2 34.5KV		
← POTENCIA DE ENTRADA			
→ POTENCIA DE SALIDA			

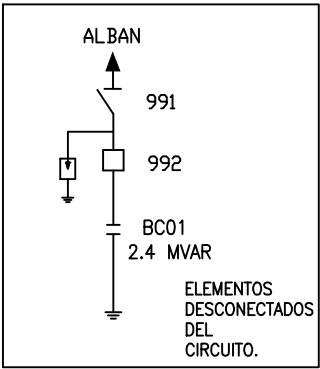

Unidad Organizativa
Administración Información
Técnica Col

REVISION No.	14
FECHA:	AGOSTO/2021
ARCHIVO:	VILLETA.DWG
C:\ESQUEMAS SUBESTACIONES\CONTROL UNIFILARES	

DIAGRAMA UNIFILAR	
SUBESTACIÓN VILLETA	
TEL. 918-445100 SIEMENS 6619	
CODIGO:	VT

60
HOJA: 1
DE: 1