


512	MEDIDA B1 LIBERIA4	→
522	D1 SIEMENS 25 MVA 34.5/13.66/11.8KV	→
532	LIBERIA6	→
12	VA11D SAN ANTONIO	→
21	D2 SIEMENS 25 MVA 34.5/13.66/11.8KV	→
32	VA12D EL TRIUNFO	→
41	MEDIDA B1.1	→
52	VA13D VIOITA	→
61	VA14D VA_SUAX_1	→
POTENCIA DE ENTRADA		→
POTENCIA DE SALIDA		→

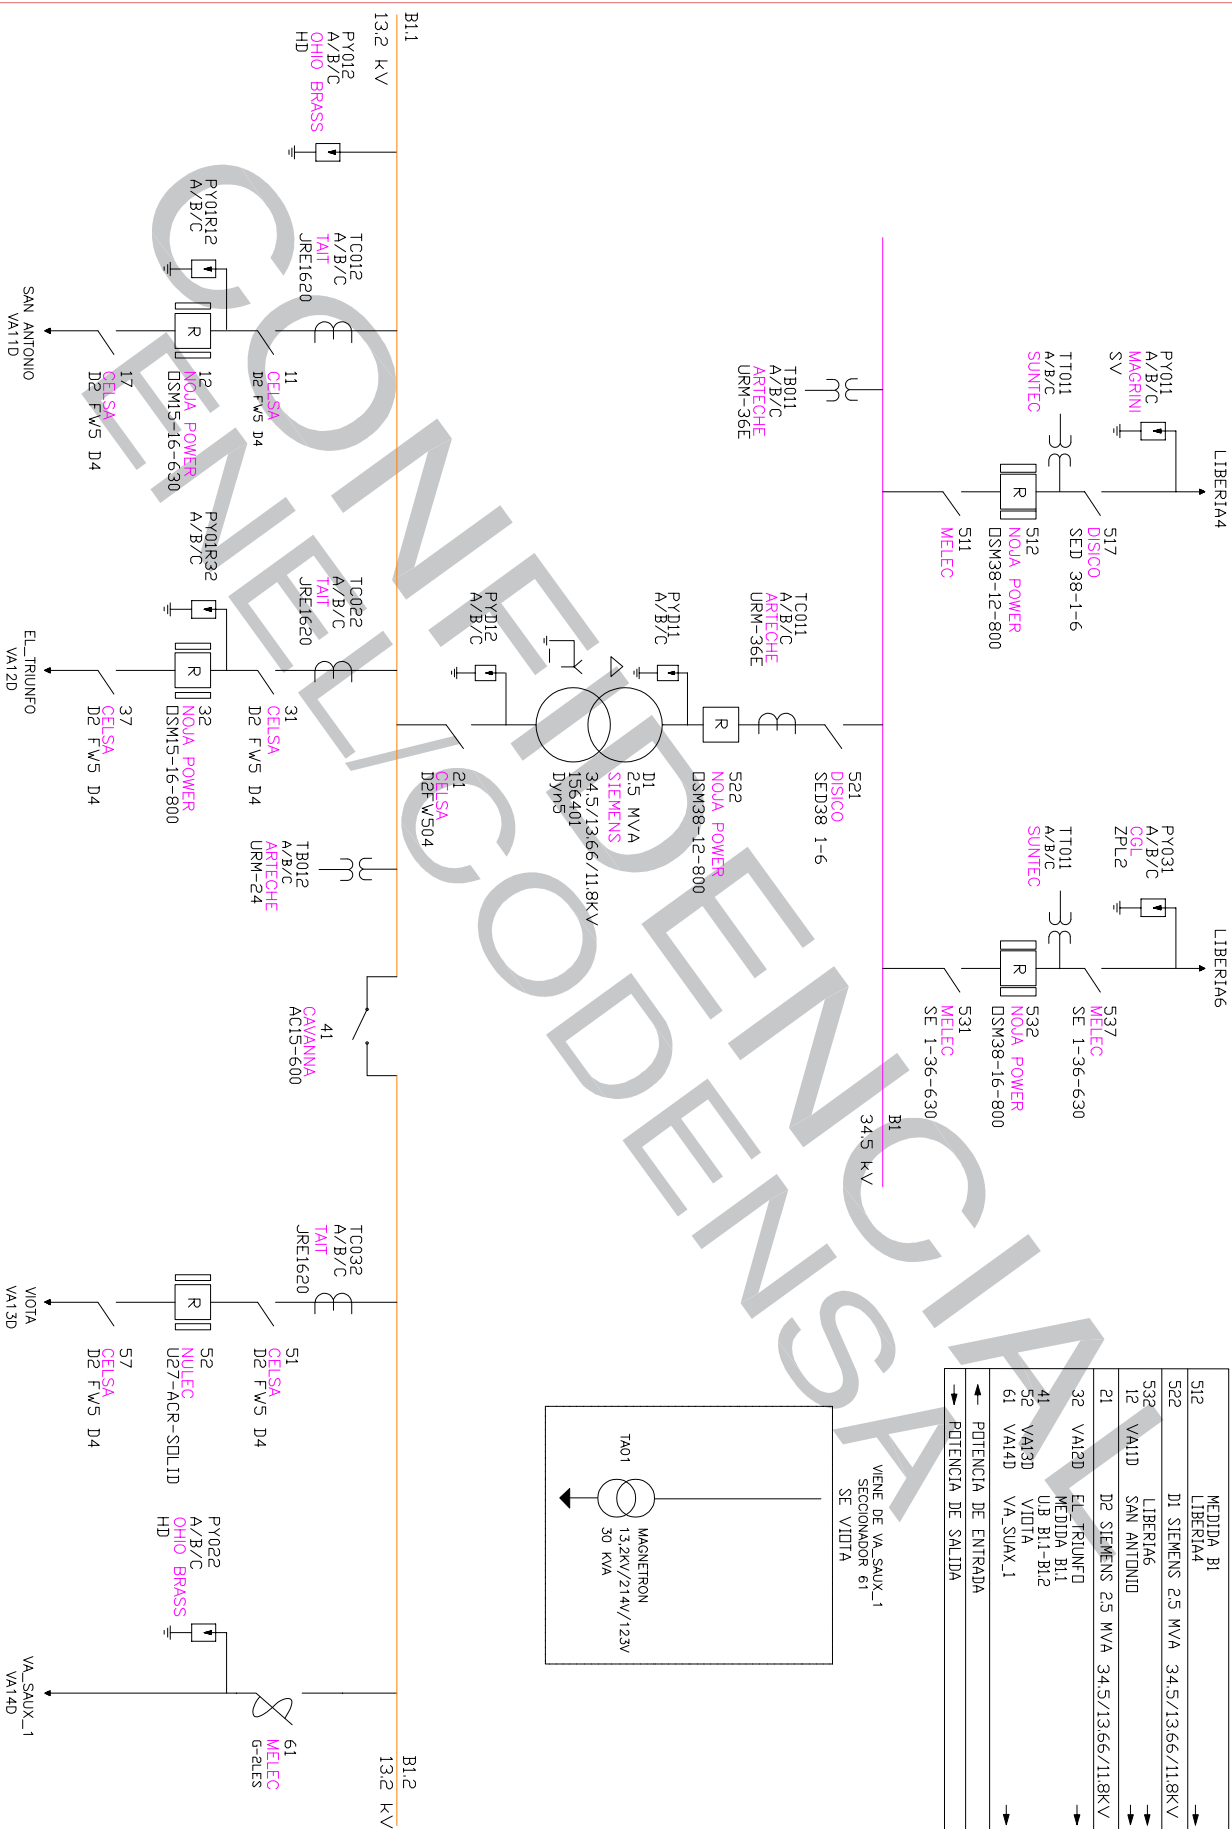

		Unidad Organizativa Administración Informática Técnica Col.	
REVISION No.	19	DIAGRAMA UNIFILAR	
FECHA:	NOVIEMBRE/2022	SUBESTACIÓN VIOITA	
ARCHIVO:	VIOITA.DWG	MUNICIPIO DE VIOITA BARRIO SALVADOR ALLENDE	
CODIGO:	VA	DE: 1	