


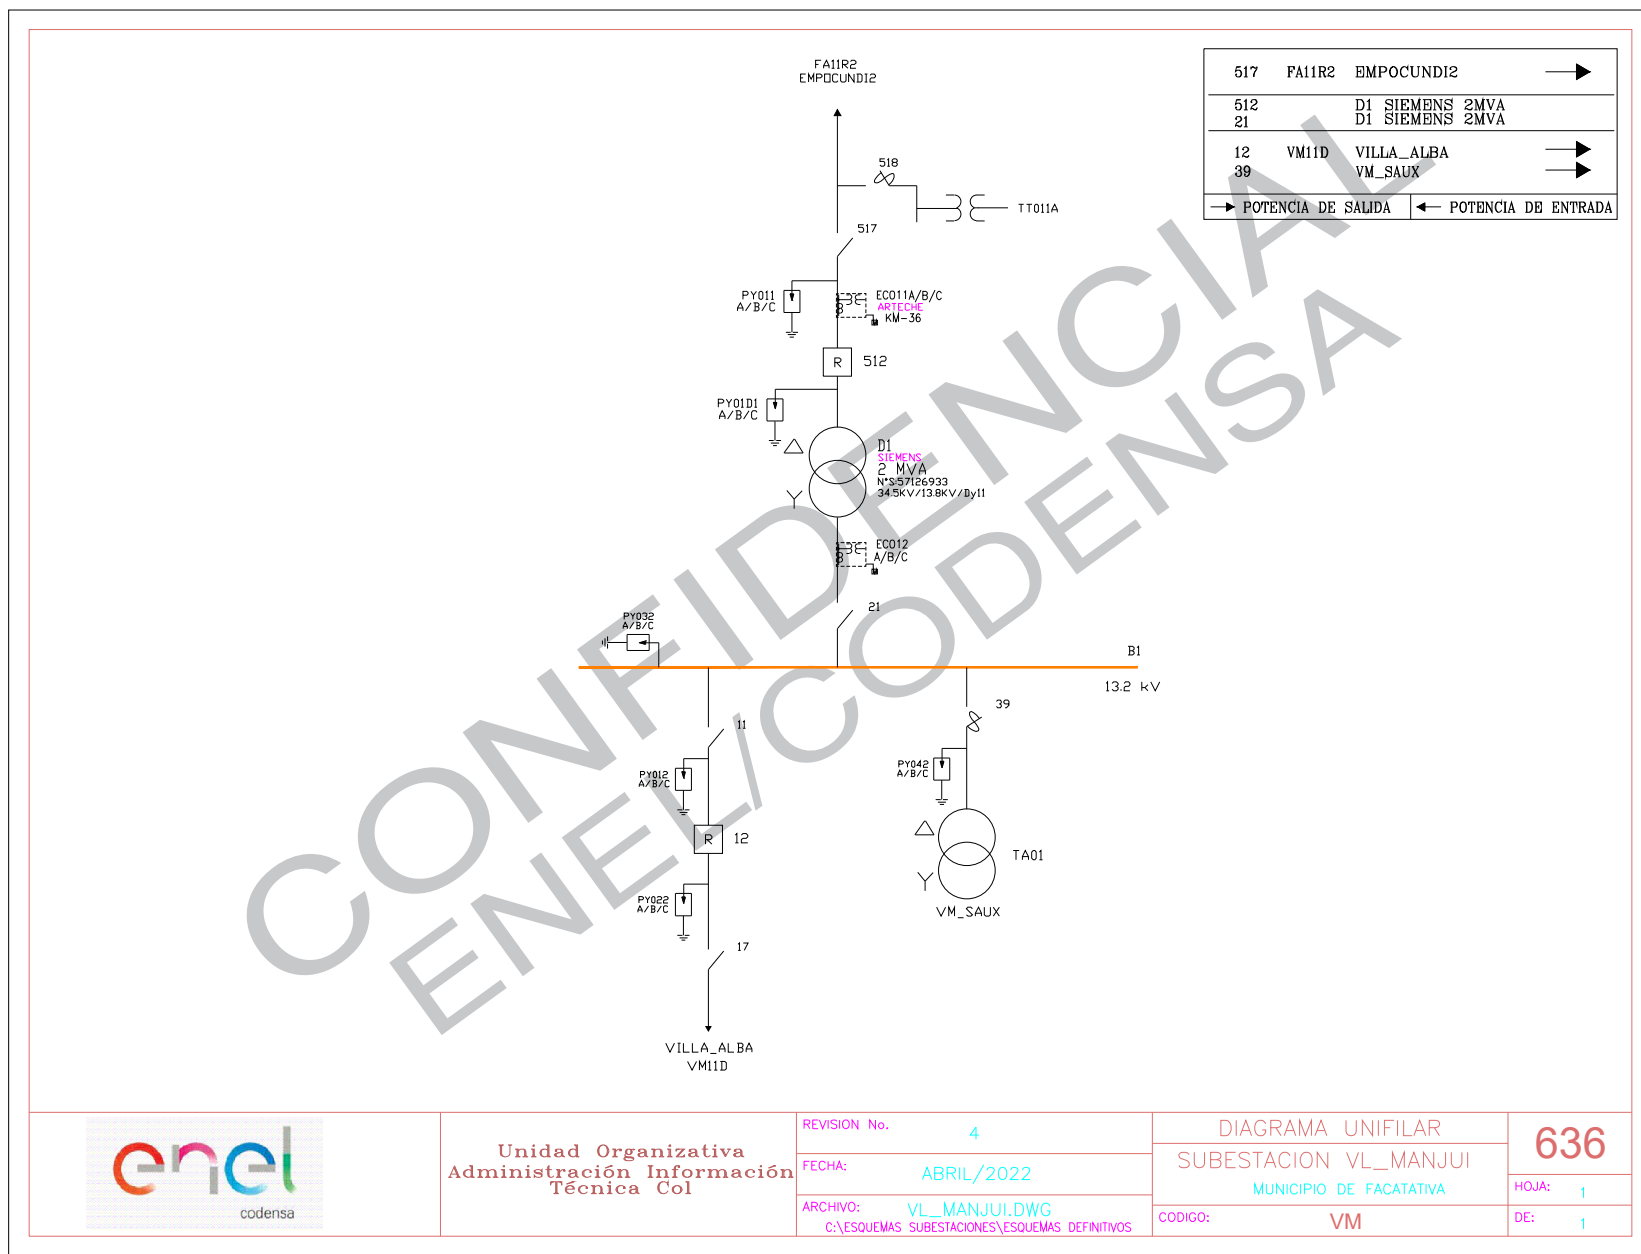

Unidad Organizativa
Administración Información
Técnica Col

REVISION No. 4
FECHA: ABRIL/2022
ARCHIVO: VL_MANJUI.DWG
C:\ESQUEMAS SUBESTACIONES\ESQUEMAS DEFINITIVOS

DIAGRAMA UNIFILAR
SUBESTACION VL_MANJUI
MUNICIPIO DE FACATATIVA
CODIGO: VM

636
HOJA: 1
DE: 1