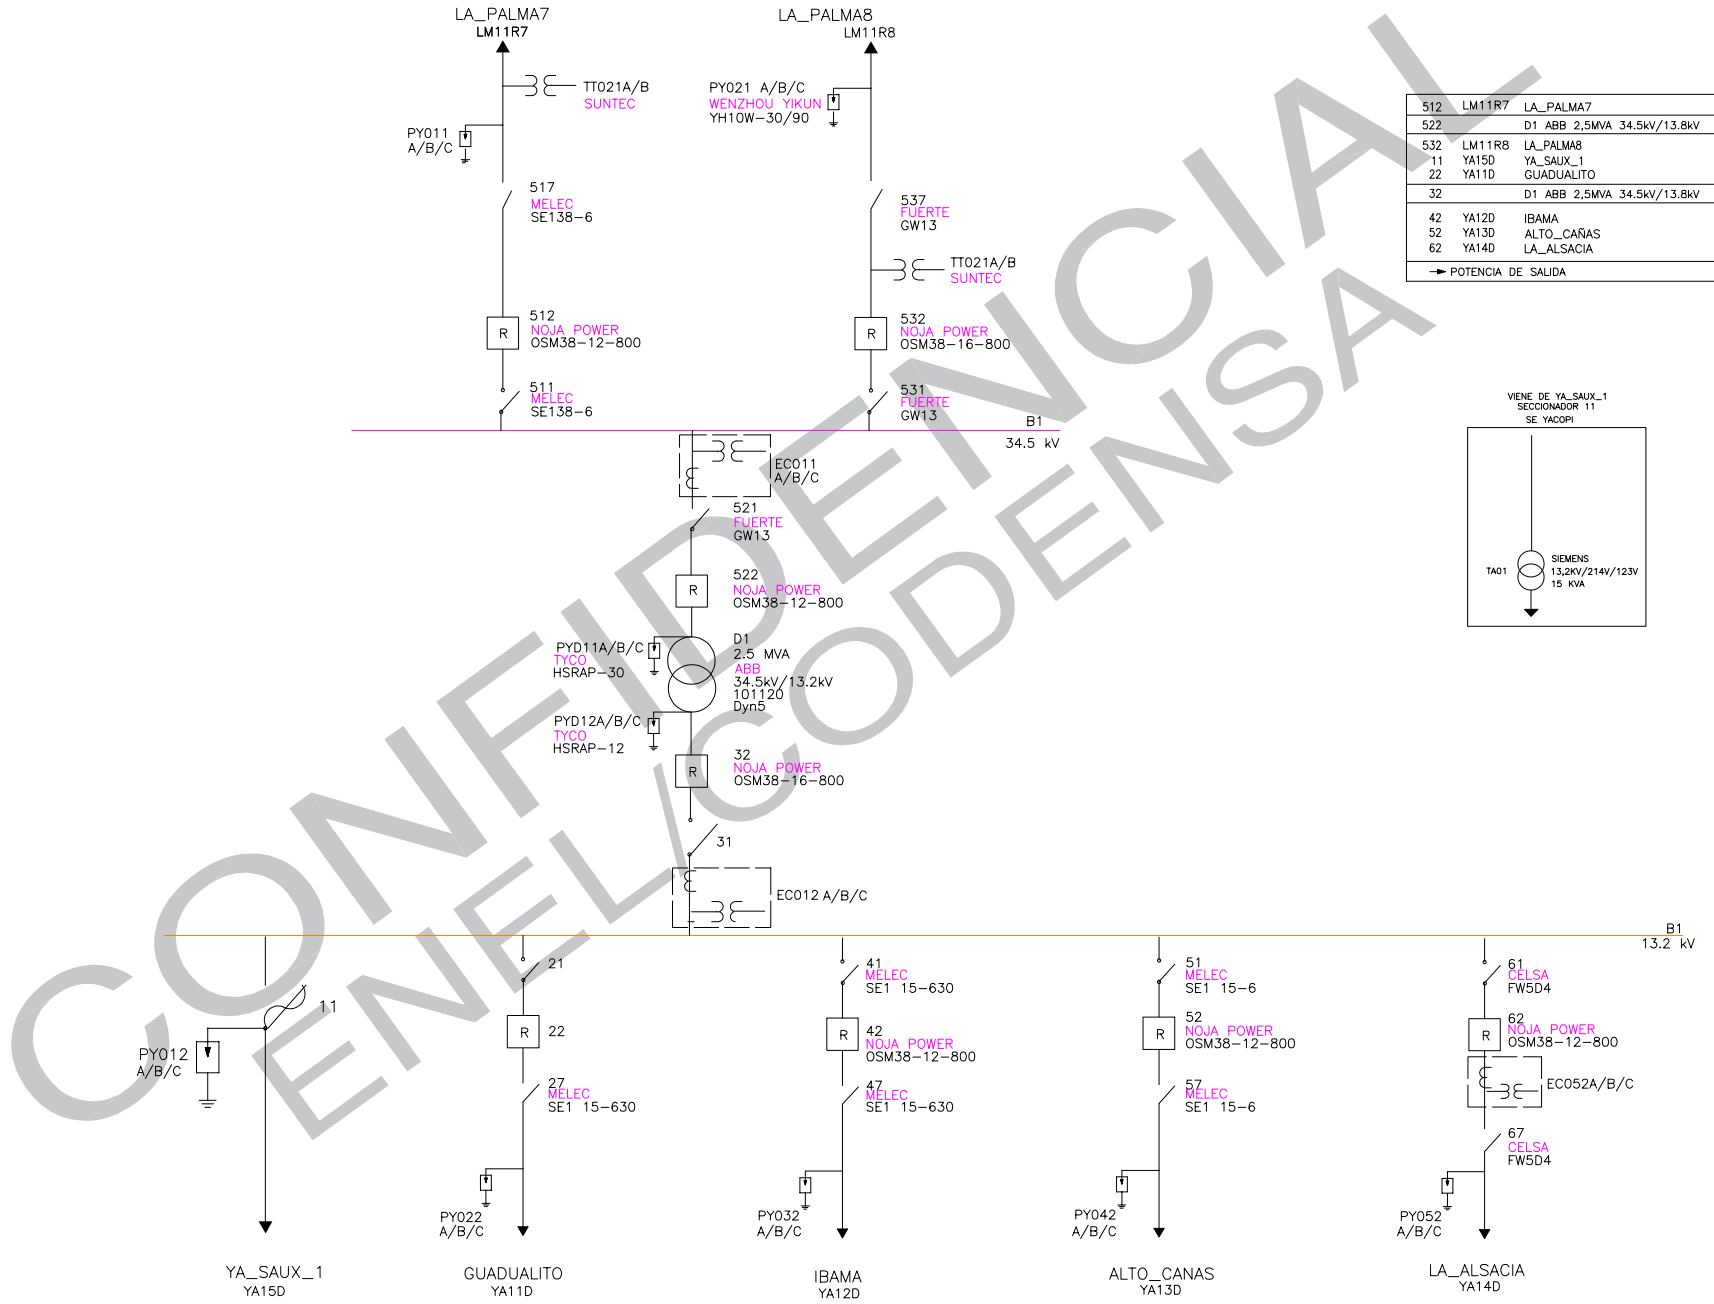


CONFIDENCIAL
ENEL CODENSA

codensa

Unidad Organizativa
Administración Información
Técnica Col.

REVISION No.	13
FECHA:	AGOSTO/2022
ARCHIVO:	YACOPI.DWG
	Y:\\FileServer\CONTROL UNIFILARES\UNIFILARES_MARZO_2019

DIAGRAMA UNIFILAR

SUBESTACION YACOPI

VEREDA EL NUPAL, MUNICIPIO DE YACOPI

CODIGO: YA

HOJA: 1

DE: 1